

OAKLAND EXCHANGE MEDICAL

SOUTHERN RAILWAY
BUILDING #9
TOWN OF OAKLAND, FL 34731

OWNER ARCHITECT/ ENGINEER OF RECORD CONTRACTOR MEP ENGINEER

THE RESTORATION PLACE CLINIC ANTONIO RENTA - CHRISTELLE RENTA 141 TERRA MANGO LOOP, SUITE B ORLANDO, FLORIDA 32835 (407) 730-0027

ELITE UNIVERSAL, LLC. ANDREW SECHLER P.A. 3210 S. ORGEOLE AVE. ORLANDO, FLORIDA 32806 (407) 325-3550

GP CONSTRUCTION PAUL GAYNOR, CGC / JEFF PAYNTER, CGC 1200 OAKLEY BEAVER BLVD. SUITE 203 ORLANDO, FLORIDA 34711 (352) 552-2823

MEP DESIGN ENGINEERING, INC. N. SAM AHMAD, P.E., LEED AP 9901 BRICK ROAD SUITE 201 WINTER PARK, FLORIDA 32792 (407) 496-6241

CIVIL ENGINEER

STRUCTURAL ENGINEER

CODE SUMMARY

Florida Building Code 8th edition (2023)
FBC Residential 8th edition (2023)
FBC Accessibility 8th edition (2023)
National Electrical Code 2020 & FBC 2023 Energy Code 8th Edition
FBC Fuel Gas Code 8th edition (2023)
FBC Existing Building Code 8th edition (2023)
FBC Florida Energy Code 8th edition (2023)
FBC Mechanical 8th edition (2023)
FBC Plumbing Code 8th edition (2023)
Florida Fire Prevention Code 8th edition
NFPA 101 Life Safety Code (2021) with Florida Amendments
NFPA 1 Uniform Code (2021) with Florida Amendments
Engineering Standards Manual, 5th Edition****

PROJECT DATA

EXISTING ZONING: PUD (COMMERCIAL)
EXISTING LAND AREA: N/A S.F. (XXX ACRES)
SURFACE AREA RATIO: (NO CHANGE)
LANDSCAPE AREA - N/A SF
IMPERVIOUS AREA - N/A SF
BUILDING GROSS SQUARE FOOT: 2,520 GSF
FLOOR AREA RATIO: N/A
BUILDING TYPE: TYPE III-B
BUILDING HEIGHT: 24'-8"
SPRINKLERED: NO

OCCUPANCY CLASSIFICATION:
BUSINESS (OFFICE MEDICAL)
PROPOSED OCCUPANCY: 27 PEOPLE

BUILDING DEPARTMENT:
TOWN OF OAKLAND PERMITTING DEPARTMENT
407-656-1117
220 N. TUBBS STREET
OAKLAND, FL 34760

CODE REFERENCE

THIS SPACE IS DEFINED AS: "NO **CHANGE OF USE**" FOR 100% OF THE SPACE

NFPA 101
43.1.1 CLASSIFICATION OF REHABILITATION WORK CATEGORIES. REHABILITATION WORK ON EXISTING BUILDINGS SHALL BE CLASSIFIED AS ONE OF THE FOLLOWING WORK CATEGORIES:
(2) RENOVATION - "GREY-SHELL" SPACE, UNOCCUPIED SCOPE OF WORK.

43.2.2.1.2 RENOVATION. THE REPLACEMENT IN KIND OR STRENGTHENING OF LOAD-BEARING ELEMENTS; OR THE REFINISHING, REPLACEMENT, BRACING, STRENGTHENING, OR UPGRADING OF EXISTING MATERIALS, ELEMENTS, EQUIPMENT, OR FIXTURES, WITHOUT INVOLVING THE RECONFIGURATION OF SPACES.

GENERAL CONSTRUCTION NOTES:

- ALL DIMENSIONS ARE TO BE FIELD VERIFIED PRIOR TO NEW CONSTRUCTION
- ALL WORK TO BE PERFORMED IN ACCORDANCE WITH THE FBC2023, THE NEC 2020, THE ZONING ORDINANCE OF ORANGE COUNTY BUILDING AND ZONING AND ALL OTHER APPLICABLE CODES AND STANDARDS
- ALL FINISHES SHALL BE FIRE CLASS B; (FLOORS, WALL, AND CEILINGS). ALL FINISHES, TEXTURES, COLORS AND DECORATIVE MATERIALS PER OWNER SPEC.
- THE CONTRACTOR AND / OR OWNER, SHALL BEAR FULL RESPONSIBILITY FOR ANY CHANGES TO AND DEVIATION FROM THESE PLANS MADE PRIOR TO OR DURING CONSTRUCTION WITHOUT PREVIOUS AUTHORIZATION FROM THE ARCHITECT.
- THE ARCHITECT DOES NOT HAVE CONSTRUCTION FIELD SUPERVISION NOR CONSTRUCTION ADMINISTRATION ON THIS PROJECT.

INDEX OF SHEETS

	100% PERMIT	RESUBMIT	DEMOC PERMIT	RESUBMIT	REVISION
A100 COVERSHEET / SITE PLAN	●				
A100 LIFESAFETY PLAN	●				
A101 LEVEL 1 FLOOR PLAN	●				
A102 BATHROOM DETAILS	●				
A103 REFLECTED CEILING PLAN	●				
A104 FLOOR FINISH PLAN	●				
A500 PARTITION TYPES AND DETAILS	●				
A520 DOOR SCHEDULE & DETAILS	●				
M000 MECHANICAL SPECIFICATIONS, ABBREVIATIONS, LEGEND & NOTES	●				
M101 MECHANICAL PLAN & SCHEDULES	●				
M501 MECHANICAL DETAILS	●				
M502 ELECTRICAL SYMBOLS, ABBREVIATIONS, NOTES & SCHEDULE	●				
E101 LIGHTING PLAN	●				
E102 POWER AND SYSTEMS PLAN	●				
E201 ELECTRICAL RISER DIAGRAMS & ELECTRICAL PANEL SCHEDULES	●				
P000 PLUMBING SPECS, ABBREVIATIONS, LEGENDS & NOTES	●				
P101 PLUMBING SANITARY PLAN	●				
P201 PLUMBING RISERS & DETAILS	●				

PROJECT SCOPE OF WORK

ARCHITECTURAL:

EXISTING GREY SHELL UNIT MASONRY BUILDING AND CONCRETE SLAB. STUCCO FINISH WALLS
NEW METAL STUD WALLS AND USG DRYWALL, MUD & TAPE JOINTS.
OFFICE MEDICAL USE, AIR CONDITIONED SPACE.
1" RIGID EXTRUDED POLYSTYRENE INSULATION AT INSIDE FACE OF EXTERIOR WALL, AND METAL 'Z' Furring STRIPS,
WITH 'X' USG DRYWALL, MUD & TAPE JOINTS, ORANGE PEEL FINISH, PRIME AND FINISH COAT PAINT
2x4 ACT DRYWALL CEILING, UPGRADED ACT, WITH BEVELED TEGULAR EDGE AND SLIMLINE GRID SYSTEM.
CUSTOM LOBBY AND ADMINISTRATION AREA MILLWORK, STAINED AND CLEARETHANE.
2cm SOLID SURFACE COUNTERTOPS IN ADMINISTRATION AREAS.
2 cm RESIN COUNTERTOP IN LAB, WITH SOLID WOOD CABINETS W/ PLASTIC LAMINATE FINISH.

NO NEW EXTERIOR WINDOW OR DOOR.

SITE:

NONE. BUILDING EXISTS IN NEW PLANNED DEVELOPMENT OFFICE PARK

ROOF:

NONE. EXISTING STANDING SEAM METAL

PLUMBING:

NEW PLUMBING SANITARY AND DOMESTIC WATER
NEW WATER METER

MECHANICAL:

(1) NEW A/C CONDENSER UNIT GROUND MOUNT ON SLAB
NEW DUCTWORK, 1" INSULATED DUCTBOARD, & R-5 FLEX-DUCT.
(1) NEW FAN COIL UNITS

ELECTRICAL:

NEW 3-PHASE POWER ELECTRICAL SERVICE AND METER.
NEW STEP-DOWN TRANSFORMER
NEW MDP PANELS, AND ELECTRICAL SUB-PANELS
NEW EMERGENCY LIGHTING.
NEW EXIT LIGHTS
NEW ELECTRICAL POWER & RISER DESIGN

FIRE SPRINKLER:

A NEW NFPA FIRE SPRINKLER SYSTEM IS NOT REQUIRED IN THIS SPACE
BUILDING TO BE UNDER FIRE ALARM, WITH HORN STROBE DEVICES

TABLE 601 FIRE-RESISTANCE RATING REQUIREMENTS FOR BUILDING ELEMENTS (HOURS)

BUILDING ELEMENT	TYPE I		TYPE II		TYPE III		TYPE IV	TYPE V	
	A	B	A	B	A	B		A	B
STRUCTURAL FRAME ^A	3 ^{B,H}	2 ^B	1	0	1	0	HT	1	0
BEARING WALLS									
EXTERIOR ^C	4	3	1	0	2	2	2 ^{B,HT}	1	0
INTERIOR	4 ^B	3 ^B	1	0	1	0			
NONBEARING WALLS AND PARTITIONS									
EXTERIOR	SEE TABLE 602								
NONBEARING WALLS AND PARTITIONS									
INTERIOR ^F	0	0	0	0	0	0	SEE SECTION 602.4.6	0	0
FLOOR CONSTRUCTION INCLUDING SUPPORTING BEAMS AND JOISTS	3 ^H	2	1 ^E	0 ^{E,I}	1 ^E	0 ^{E,I}	HT	1	0 ^I
ROOF CONSTRUCTION INCLUDING SUPPORTING BEAMS AND JOISTS	1 ^{1/2} , C ^H	1 ^{C,D}	1 ^{C,D}	0 ^D	1 ^D	0 ^D	HT	1 ^{C,D}	0

MINIMUM INTERIOR FINISH CLASSIFICATION: FROM TABLE 803.5

OCCUPANCY GROUP	SPRINKLERED			UNSPRINKLERED		
	Exit			Exit		
	Exit ¹	Access	Other Spaces	Exit ¹	Access	Other Spaces
A	B	B	C	A	A	B
B	B	C	C	A	B	C
E	B	C	C	A	B	C
F	C	C	C	B	C	C
H	B	C	C	Sprinkler required		
I Restrained	B	C	C	A	B	B
I Unrestrained	B	B	B ³	A	A	A
M/D	B	C	C	A	B	C
R ^{1,4}	B	B	C	C	C	C
S	C	C	C	B	C	C

BUILDING AND CONSTRUCTION DATA

OCCUPANCY CLASSIFICATION (FBC 304)
BUILDING CONSTRUCTION TYPE (FBC TABLE 503)

GROUP B - BUSINESS (OFFICE MEDICAL)
TYPE III B, NOT SPRINKLERED

BUILDING 1 AREA: 2,520 GROSS SQ. FT.

TOTAL AREA: 2,520 GROSS SQ. FT.

BUILDING #1 - (NEW BUILDING)
OCCUPANT LOAD: BUSINESS @ 150SF/PERSON: 27 PEOPLE
OCCUPANT LOAD: 27 PEOPLE

BUILDING TO BE OF NON-COMBUSTIBLE MATERIALS AND ANY OTHER MATERIAL ALLOWED BY CODE
ALTERATION CLASSIFICATION: NEW CONSTRUCTION.

FIRE RESISTANCE

MATERIALS/CONSTRUCTION (FBC 704.3.1)

SINGLE OCCUPANCY BUILDINGS

MINIMUM FIRE RESISTANCE, FBC TABLE 705.1.2

	WALLS	OPENINGS
FIRE WALLS	1	3/4
TENANT SPACE	1	3/4
HORIZONTAL EXIT	1	3/4

INTERIOR FINISHES, FBC 803

CLASSIFICATION, FBC 803.2

A-FLAMESPREAD 0-25, SMOKE DEV. 0-450
B-FLAMESPREAD 26-75, SMOKE DEV. 0-450
C-FLAMESPREAD 76-200, SMOKE DEV. 0-450
EXITS - CLASS A
ACCESS - CLASS B
OTHER SPACES - CLASS C

OCCUPANCY (BUSINESS, NOT-SPRINKLERED),
TABLE 803.11

FIRE PROTECTION SYSTEMS FBC 903, 905

SPRINKLERS, FBC 903

DESIGN STANDARD NFPA 13 AS
MODIFIED BY NFPA 231, NFPA 231C

GROUP B - BUSINESS (OFFICE MEDICAL)
NO (N/A)

OCCUPANCY REQUIREMENTS, FBC 903.7

FIRE ALARMS, FBC 905

FIRE ALARM

FIRE SPRINKLERS

PLUMBING, MINIMUM FACILITIES FBCP, PLUMBING, TABLE 403.1

OCCUPANCY - B /BUSINESS (27 PEOPLE) - (BUILDING #1, NEW BUILDING)

	ADA UNISEX	MEN	WOMEN	REQUIRED/PROVIDED
WATER CLOSETS MEN (1/25)	-	-	-	0/0
WATER CLOSETS (WOMEN) (1/25)	-	-	-	0/0
LAVATORIES (1/80)	2	-	-	1/2
UNISEX BATHROOM WITH LAVATORY (1/25)	2	-	-	1/2
DRINKING FOUNTAINS (1/100)	-	-	-	(Y)
SERVICE SINK (Y)	-	-	-	(Y)

MEANS OF EGRESS

OCCUPANT LOAD, FBC TABLE 1004.5

BASEMENT/GRADE AREAS, OPEN TO PUBLIC

TRAVEL DISTANCE (NOT-SPRINKLERED) FBC 1017.2

EGRESS WIDTH/PER OPENING SERVED

MINIMUM CLEAR OPENING DOORS


ARRANGEMENT AND NUMBER, FBC 1004

MINIMUM NUMBER OF EXITS, FBC 1019.1

EGRESS PROVIDED - (BUILDING #1)

27 OCCUPANTS (27x 2) = 5.4" REQUIRED | (3) EXITS @ 34" & 68" = 102" PROVIDED






2 DIRECT EXITS DISCHARGING TO STREET

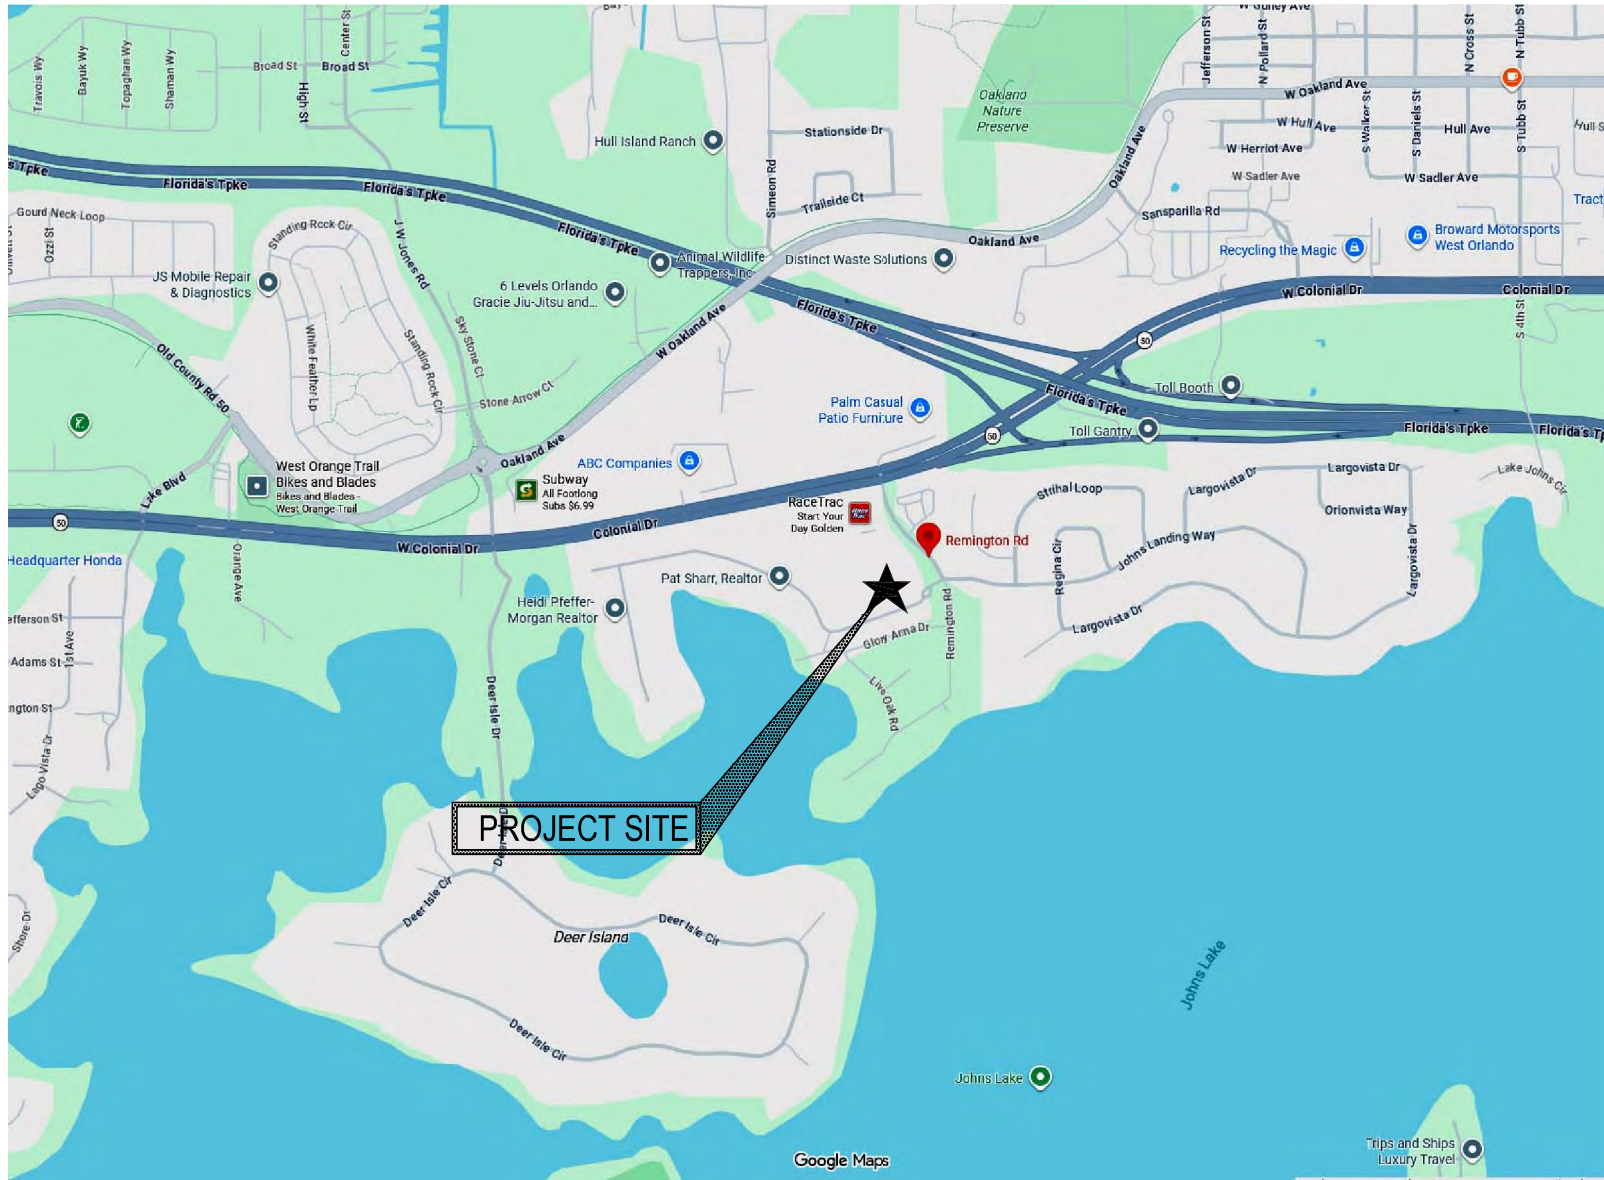

SCALE: NOT TO SCALE | 06

CODE SUMMARY

SCALE: 1/4"=1'-0" | 01

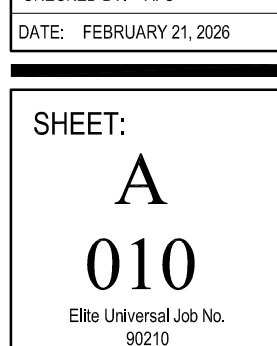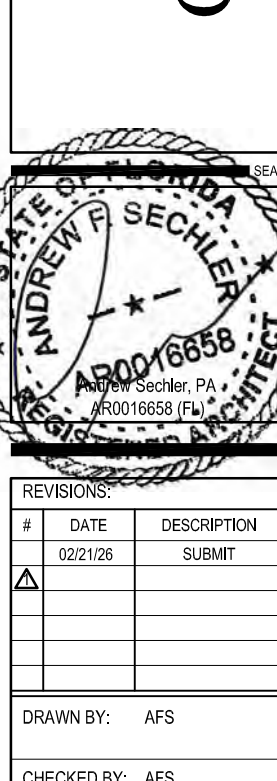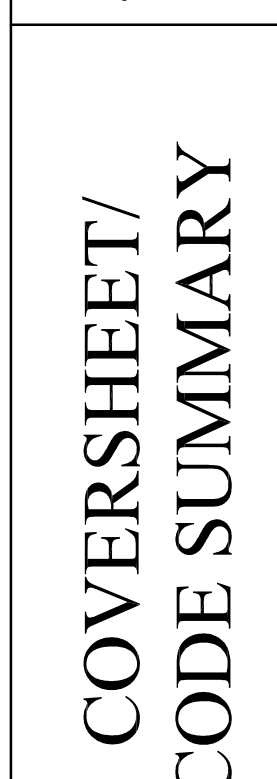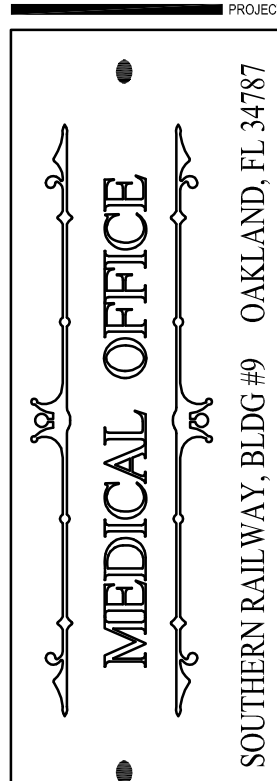 



1 POSTED MAX. OCCUPANT LOAD
SIGN: OCC. LOAD 27 PERSONS

- _____


TOTAL OCCUPIED GROSS SF	2,520 SF
BUSINESS (B)	2,175 SF


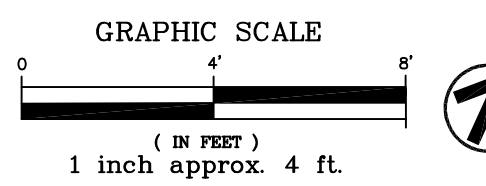


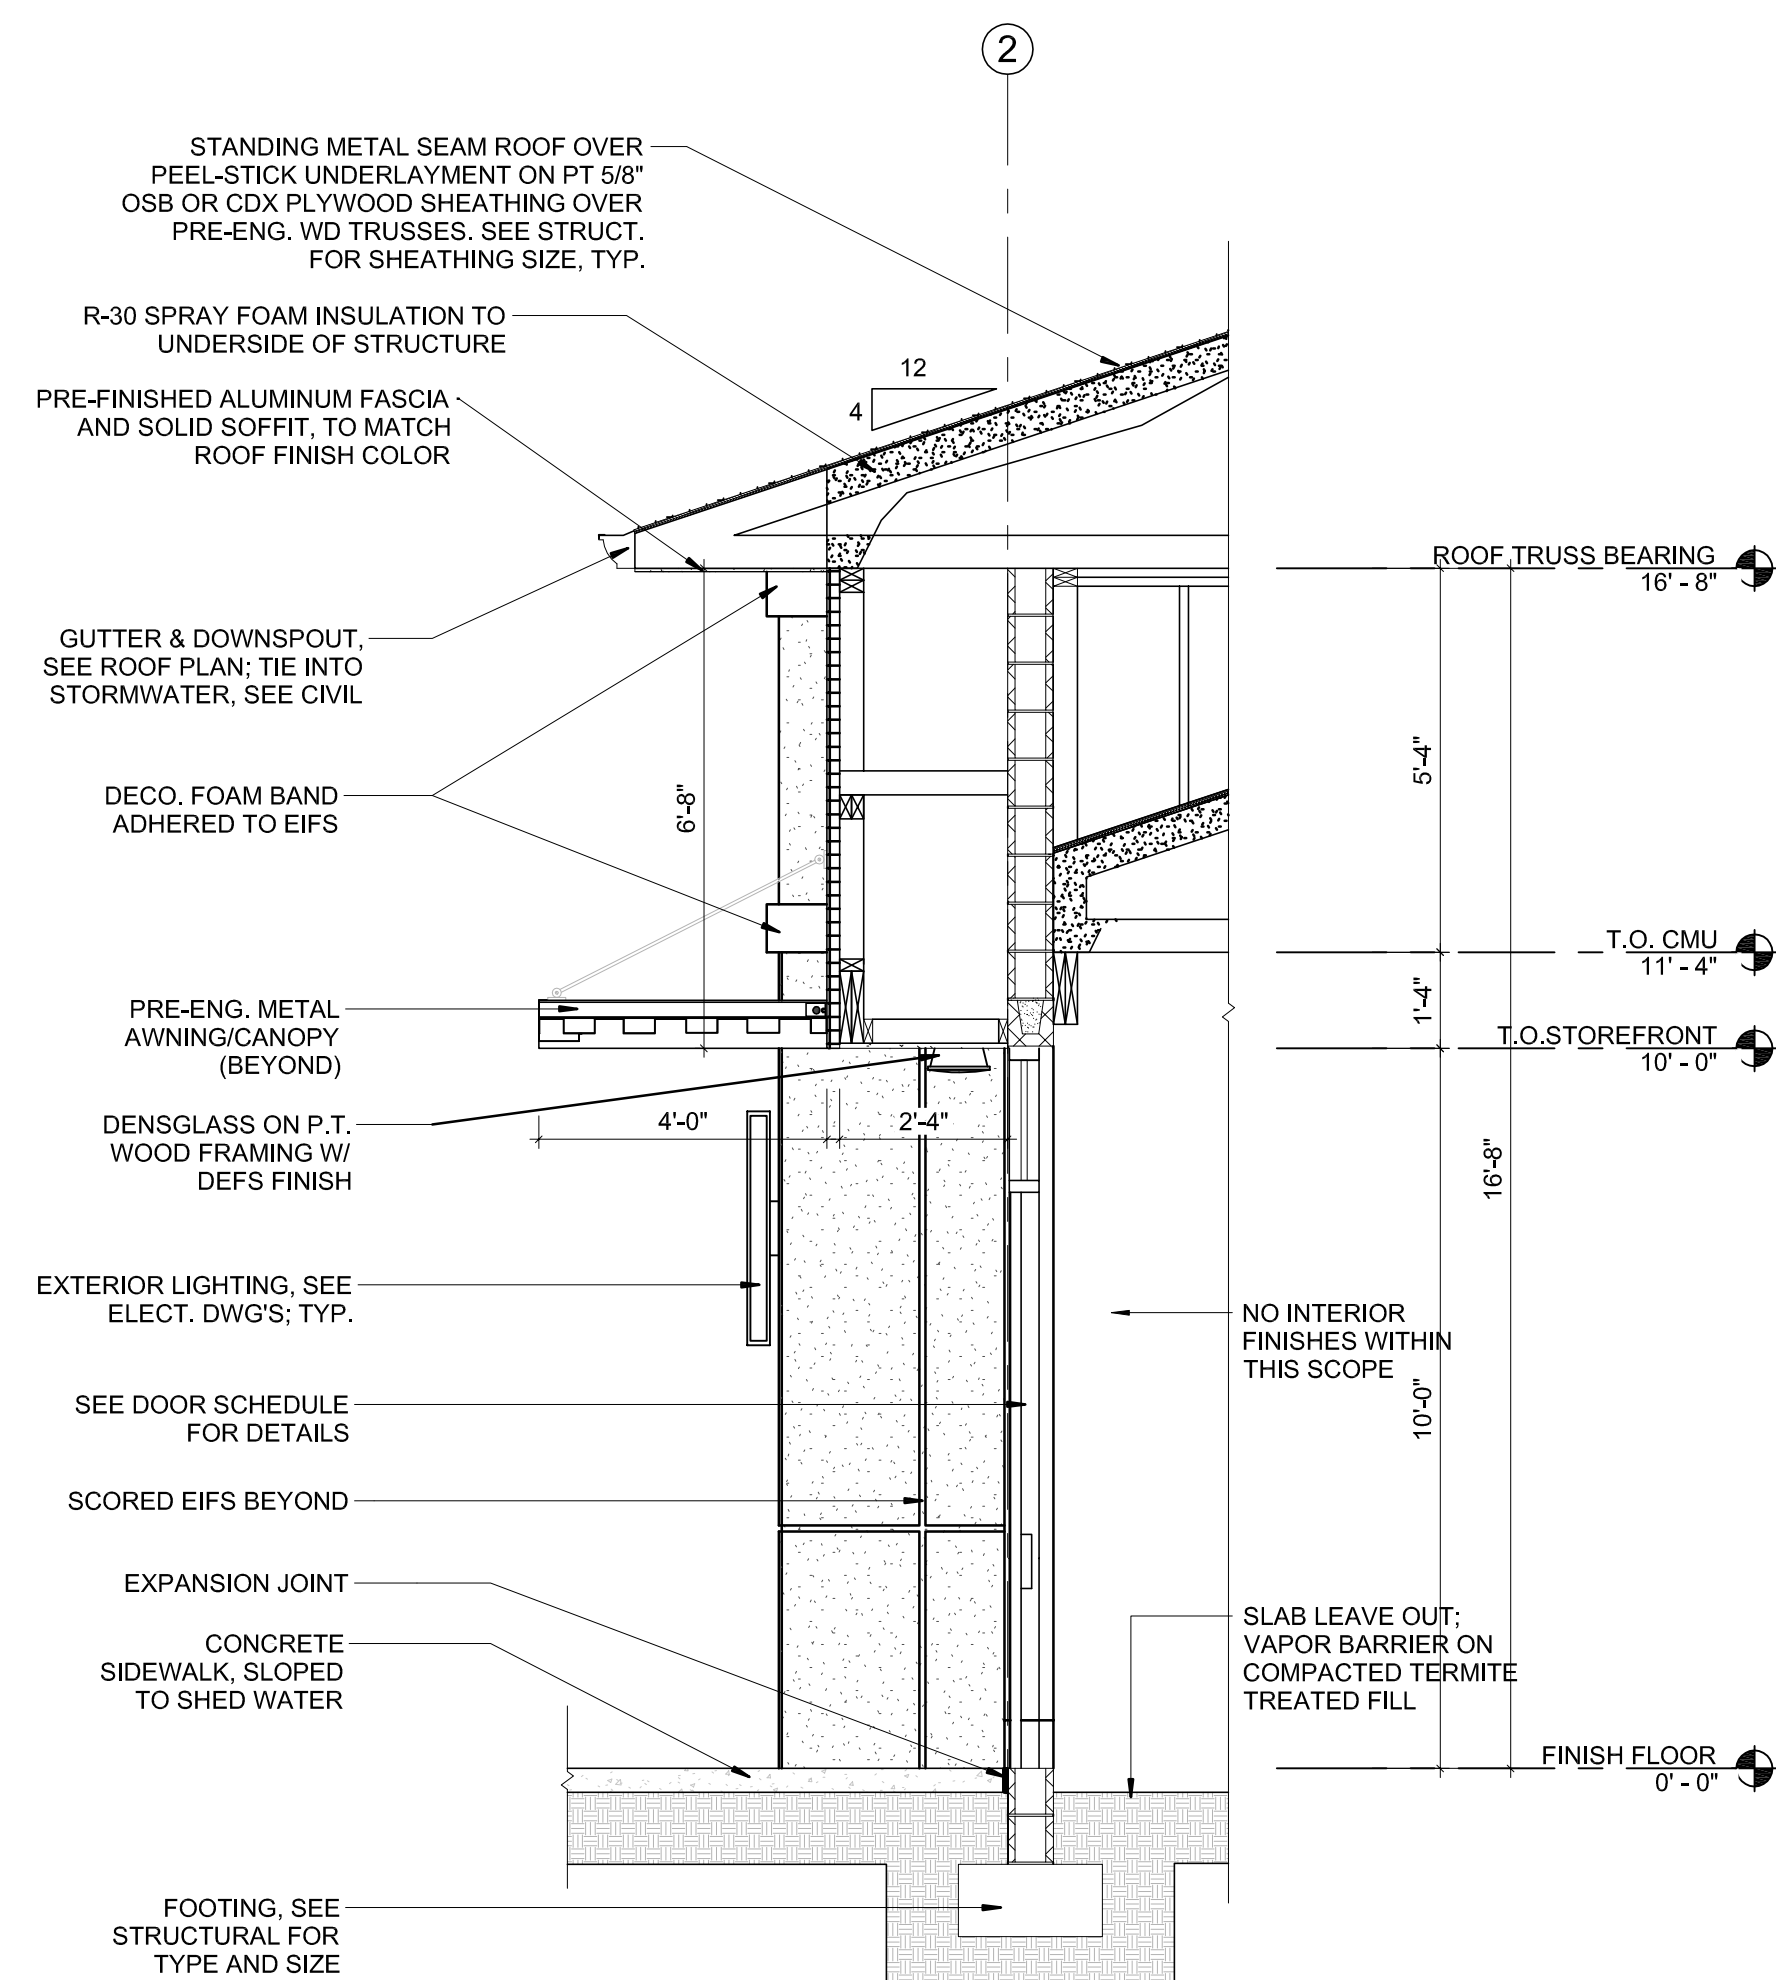






SCALE: 1/4"=1'-0"	21
-------------------	----

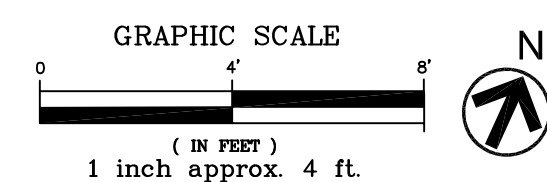

SCALE: 1/4"=1'-0"	01
-------------------	----

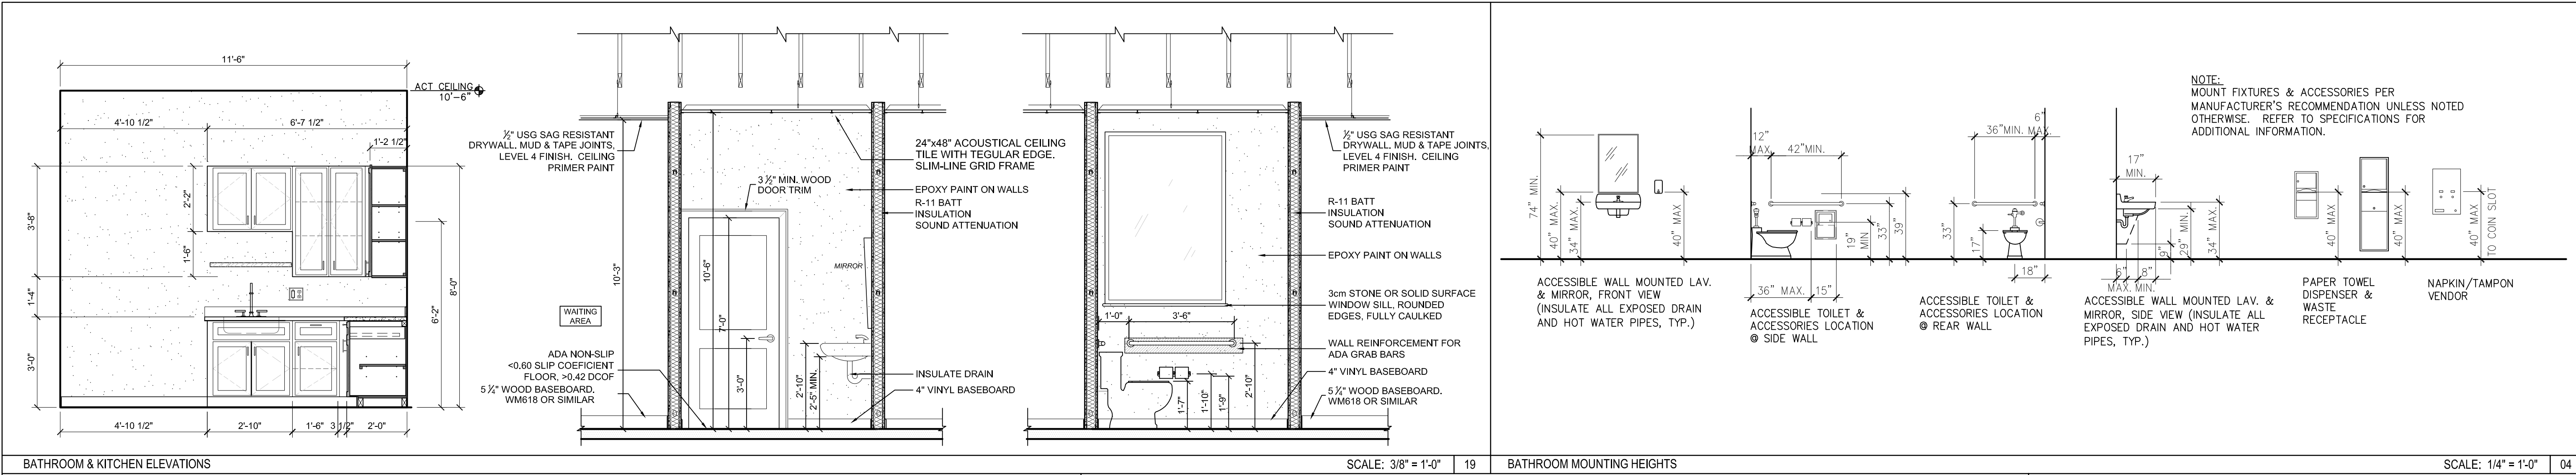

PLUMBING FIXTURE SCHEDULE									
FIXTURE NO.	FIXTURE TYPE	WASTE CONN.	TRAP	VENT CONN.	C.W. CONN.	H.W. CONN.	MANUFACTURER / MODEL #	DESCRIPTION	
WC-1	WATER CLOSET ADA TANK	3"	INTEG.	2"	1/2"	—	AMERICAN STANDARD CADET-2467.016	TANK TYPE WATER CLOSET, ELONGATED PRESSURE ASSISTED, 1.6 GPF, ELONGATED BOWL, PRESSURE ASSISTED, FLOOR MOUNTED, CLOSED COUPLED COMBINATION, BOLT CAPS, 'BRASSCRAFT' ANGLE STOP SUPPLY & ESCUTCHEON, 'OLSONITE' #95 WHITE SEAT. FLUSH HANDLE TO BE ON OPEN SIDE OF TOILET CLEAR SPACE.	
S-1	KITCHEN SINK	1-1/2"	1-1/4"	1-1/2"	1/2"	1/2"		SWISS MADISON 'RAVI' 22" TOP MOUNT STAINLESS STEEL SINK	
L-2	LAVATORY — ADA TYPE 2 HANDLE FAUCET	1-1/2"	1-1/4"	1-1/2"	1/2"	1/2"	AMERICAN STANDARD 0355.012	LUCERNE 20" x 18" WALL HUNG, VITREOUS CHINA WITH INTEGRAL BACKSPASH. 'AMERICAN STANDARD' MODEL: 7385.003.002_V05, SINGLE CONTROL LAVATORY FAUCET, RELIANT 3 FAUCET WITH LEVER HANDLE, GRID STRAINER WITH TAILPIECE, C.P. BRASS P-TRAP WITH WALL ARM & ESCUTCHEONS, 'BRASSCRAFT' ANGLE VALVE SUPPLY RISERS W/LOOSE KEY STOPS, INSULATE P-TRAP AND SUPPLIES WITH 'TRUEBRO' INSULATION KIT, 'ZURN' 1231 CAST IRON FLOOR MOUNTED CARRIER FITTING WITH CONCEALED ARMS.	
EW-1	ELECTRIC WATER COOLER	2"	1-1/2"	1-1/2"	1/2"		ELKAY EZ08	SINGLE WALL MOUNTED STAINLESS STEEL BASIN & PEWTER VINYL COVERED COOLER, CAPACITY TO DELIVER 8 GPH OF 50°F. WATER WITH INLET TEMP. OF 80°F AND ROOM TEMP. OF 90°F., W/ 1/5 HP., 120V, 60 CYCLE, 1 PH. W/ OVERLOAD PROTECTION 1 1/2" P-TRAP STOP VALVE, CORD & PLUG. ZURN #Z1225 CAST IRON FLOOR MOUNTED CARRIER FITTING WITH BEARING PLATE.	
US-1	UTILITY SINK	3"	3"	1-1/2"	1/2"	1/2"	FIAT FL-1	FLOOR MOUNTED SERV-A-SINK WITH WHITE BAKED ENAMEL ANGLE LEGS THAT SLIP INTO MOLDED SOCKETS FOR RIGID, FRICTION-FIT, A-1 DECK PLATE TYPE FAUCET.	
NOTE:	ALL PLUMBING FIXTURES SHALL BE SUPPLIED WITH WATTS "FLOODSAFE" AUTO-SHUT OFF CONNECTOR TYPE SUPPLY RISERS WITH BRAIDED STAINLESS STEEL CONNECTORS. THIS SHALL INCLUDE ALL FAUCETS, TOILETS, WASHING MACHINES, DISHWASHERS & ICE MAKERS. PROVIDE FULLY ACCESSIBLE SHOCK ARRESTORS ON SUPPLIES TO WASHING MACHINES, ICE MAKERS AND DISHWASHERS.								

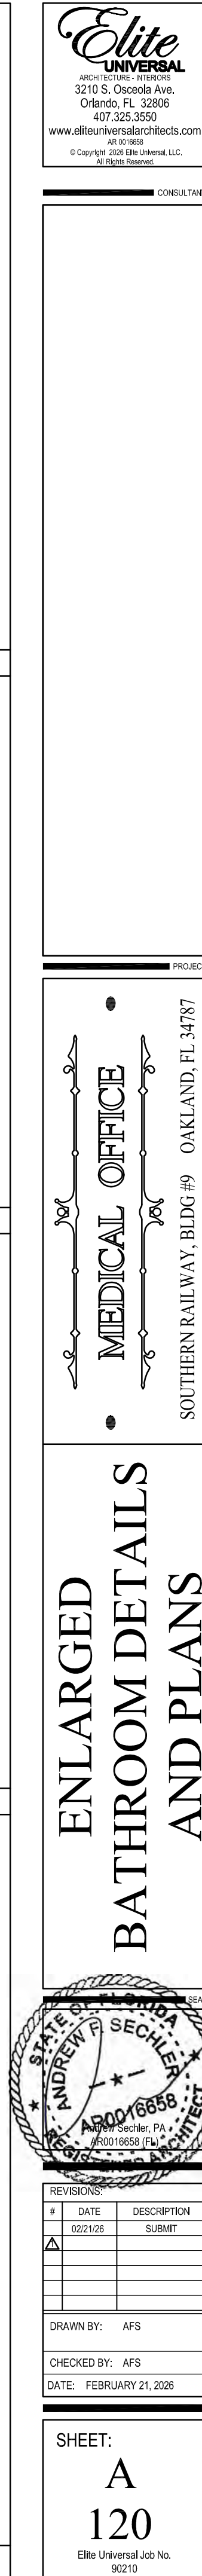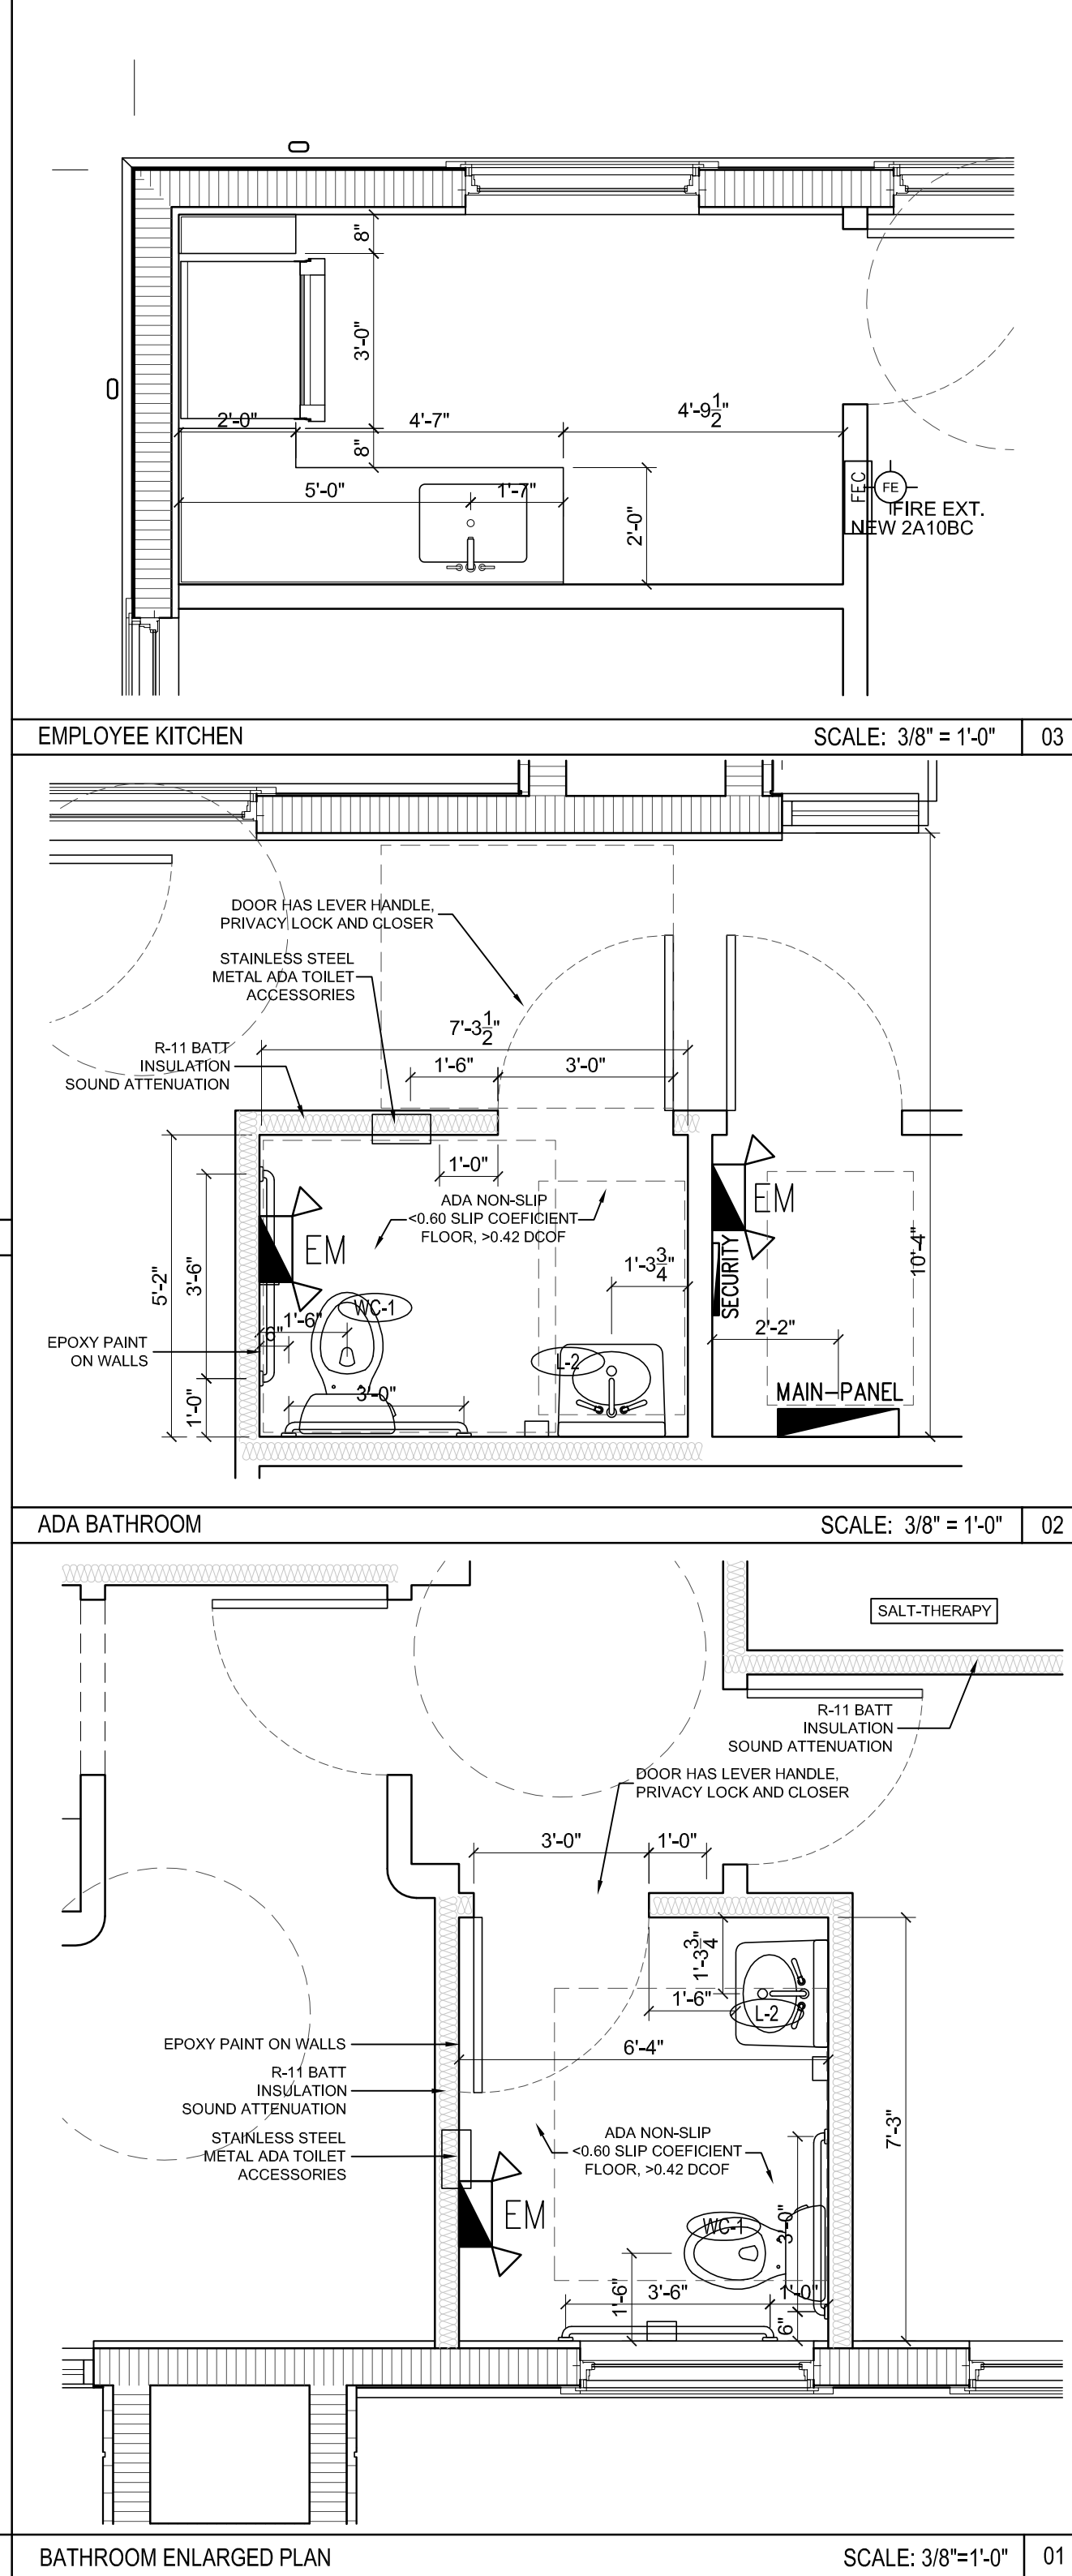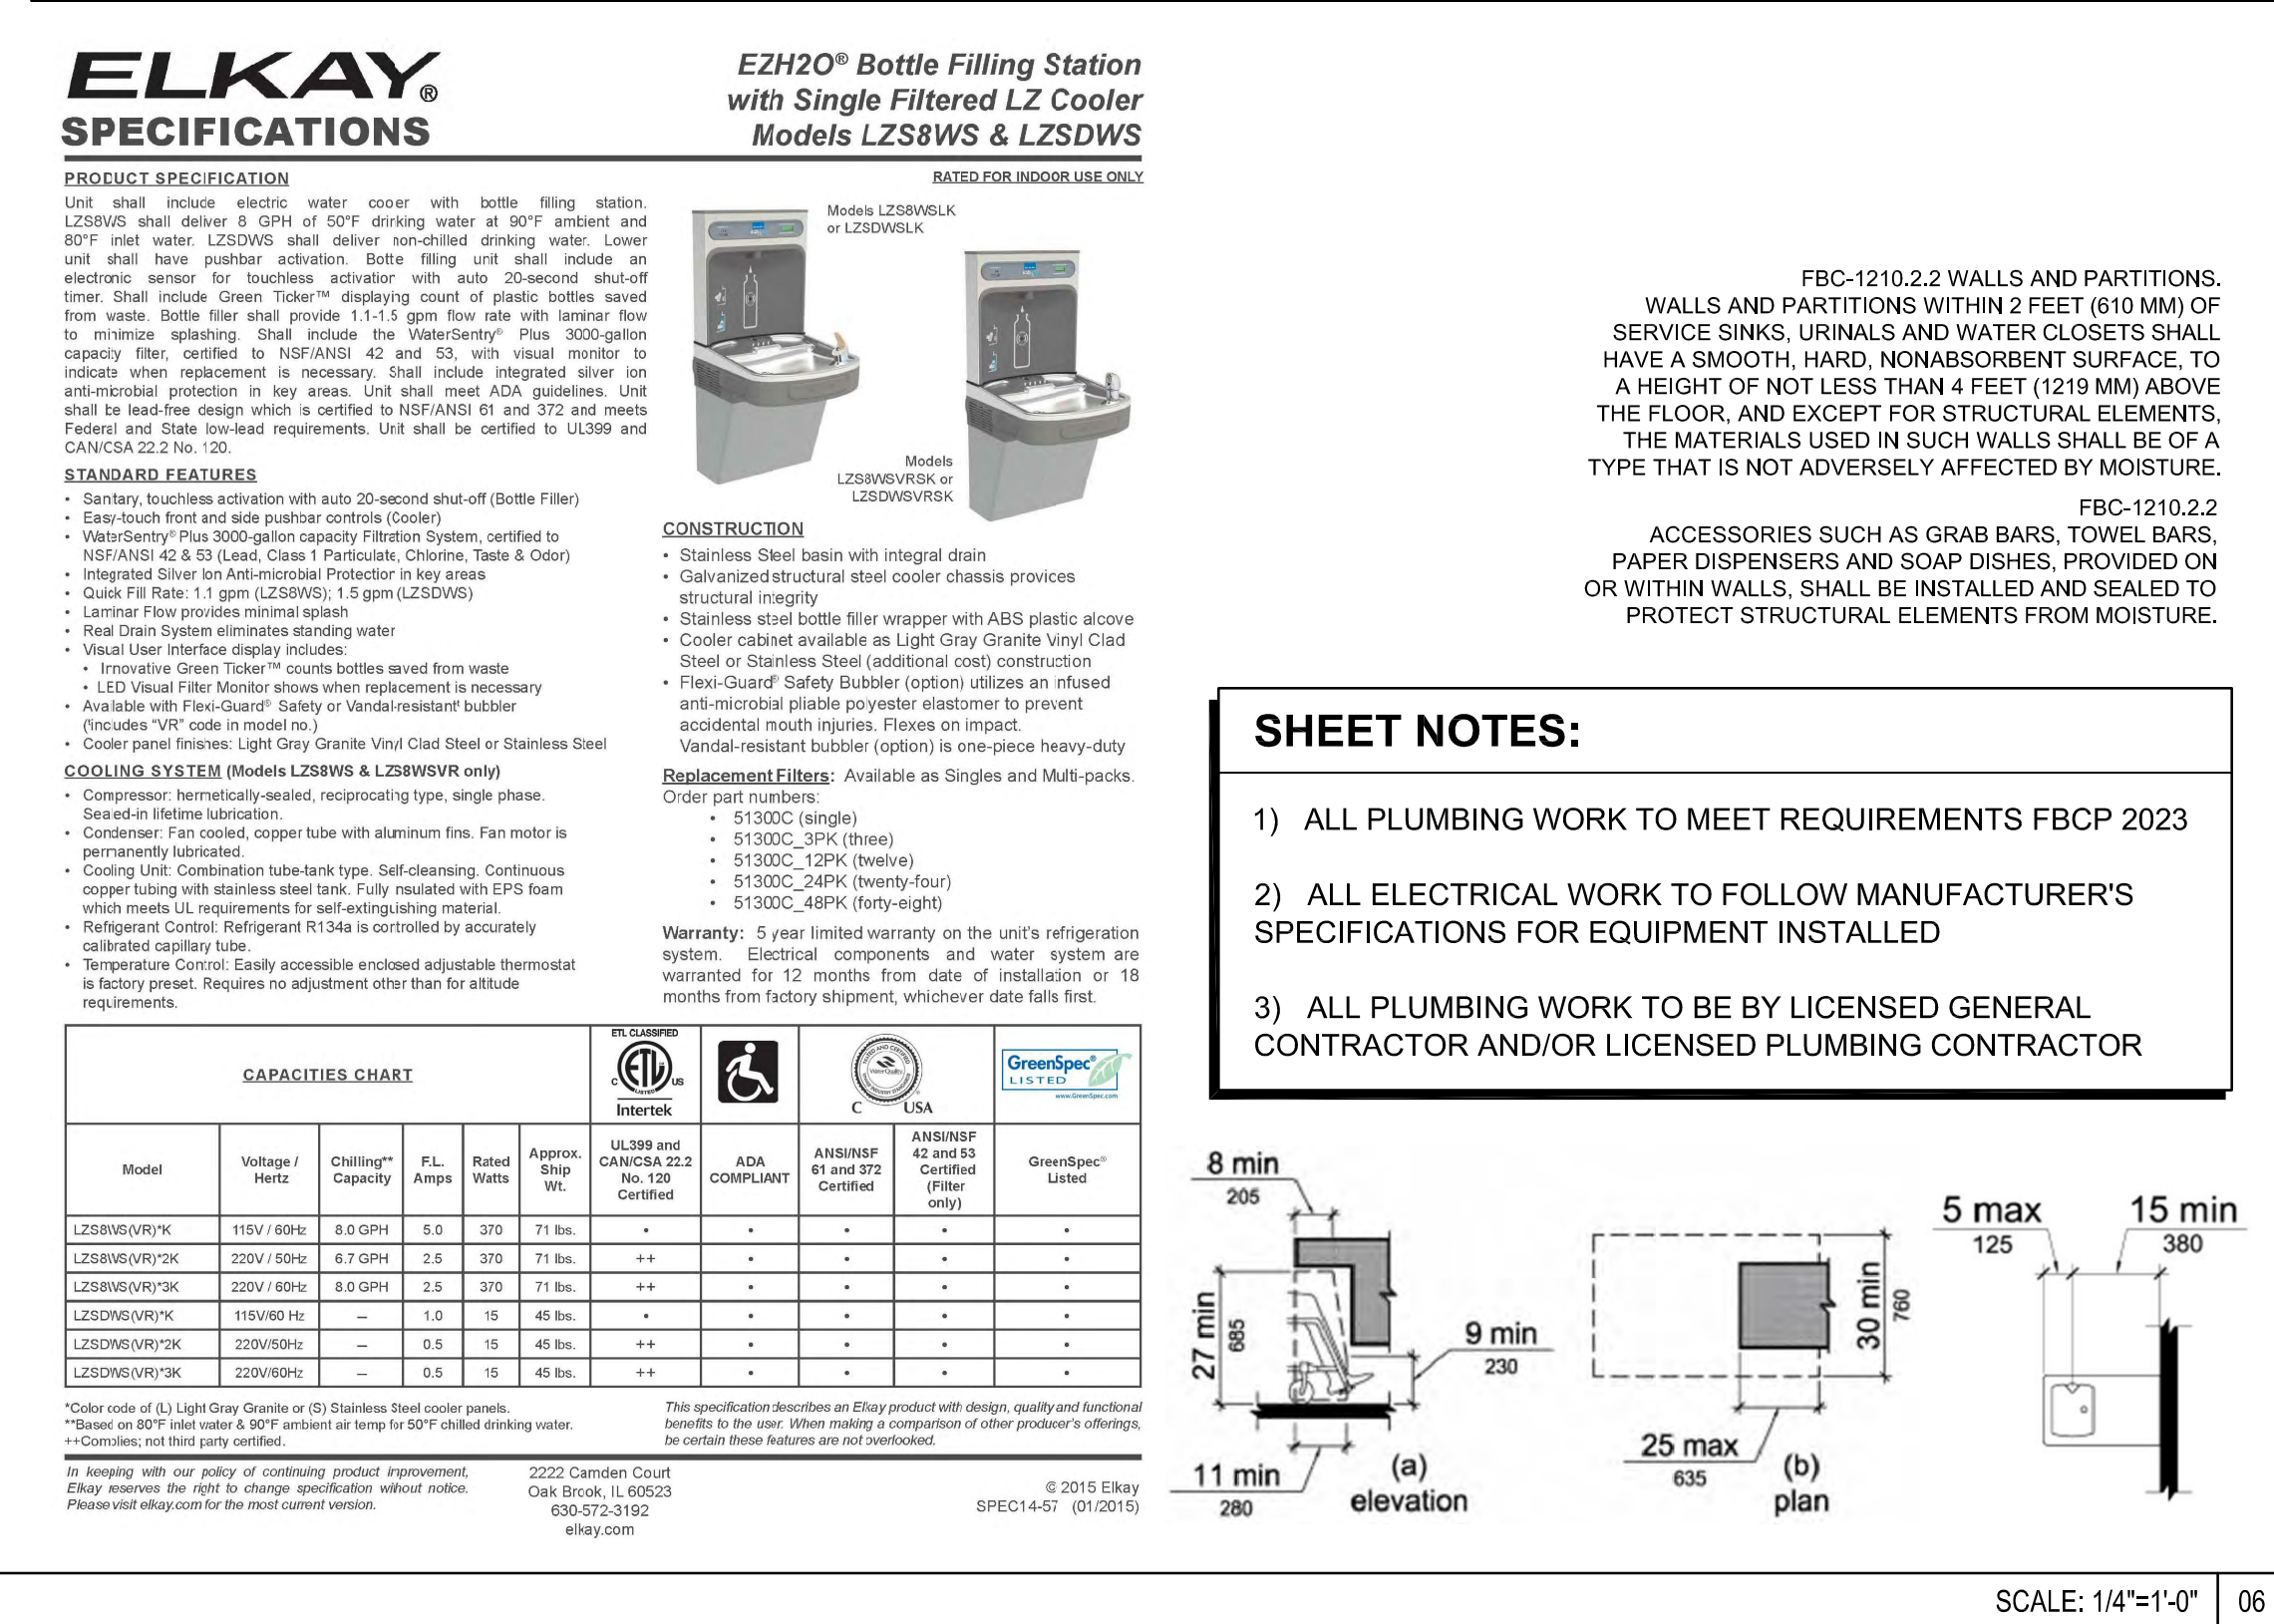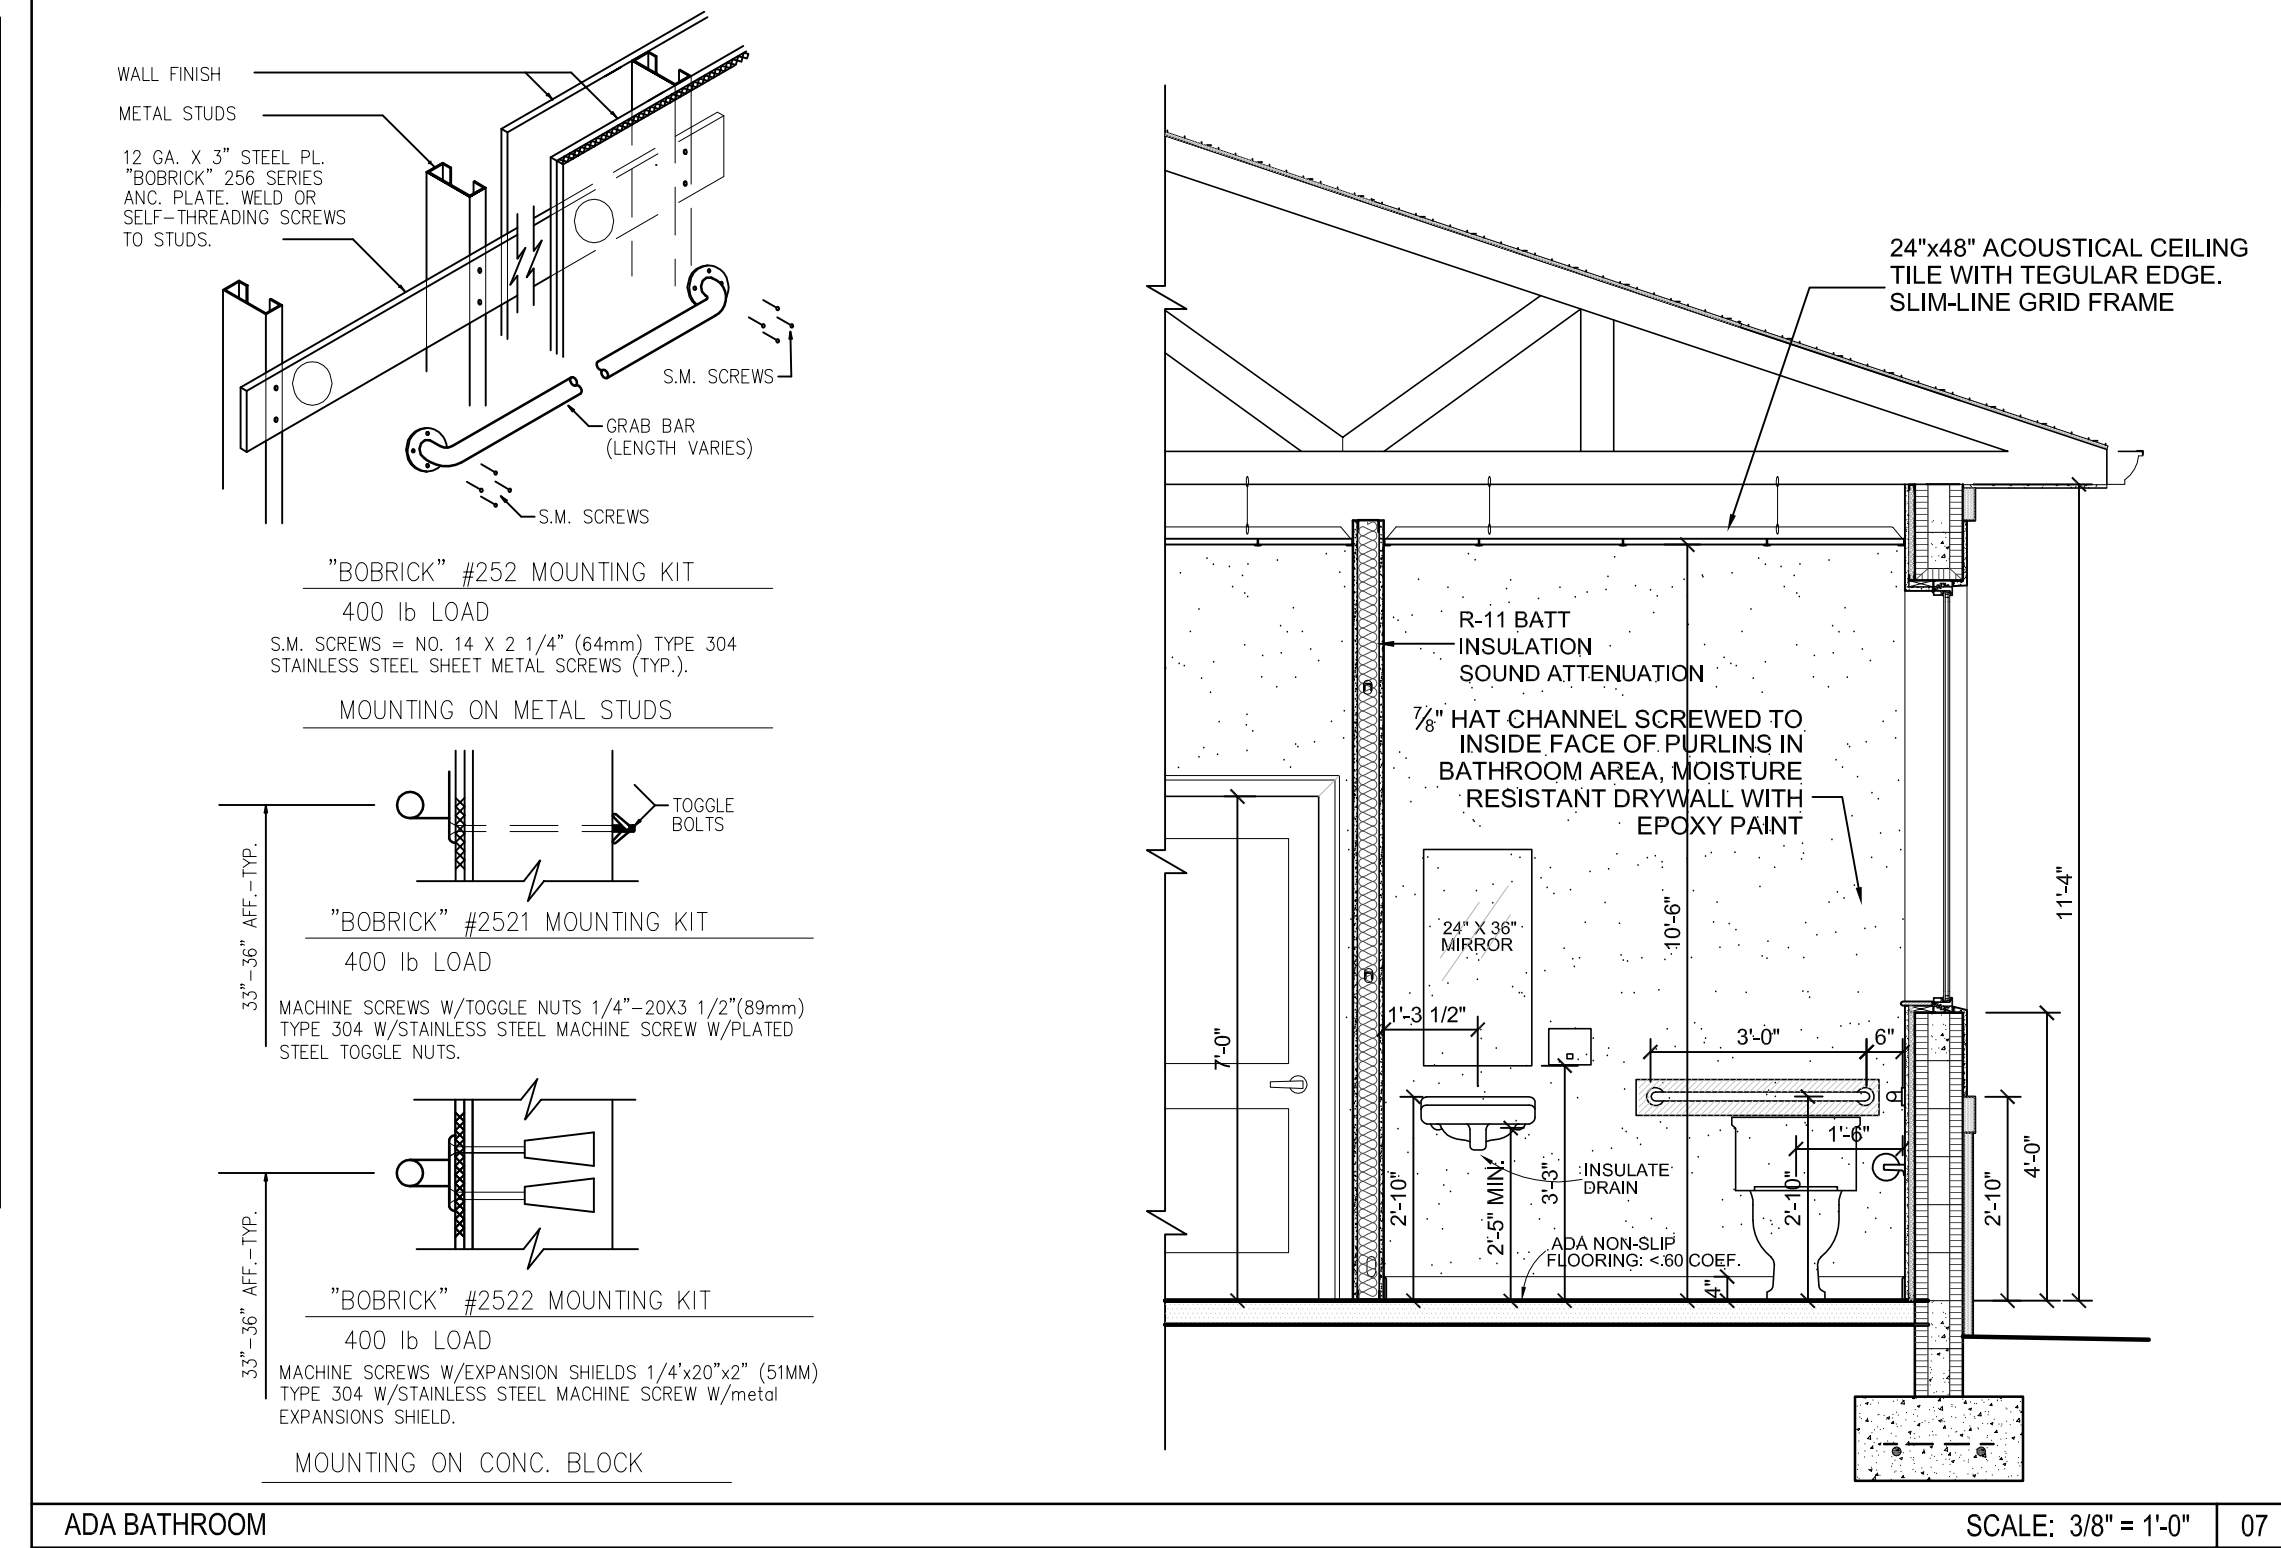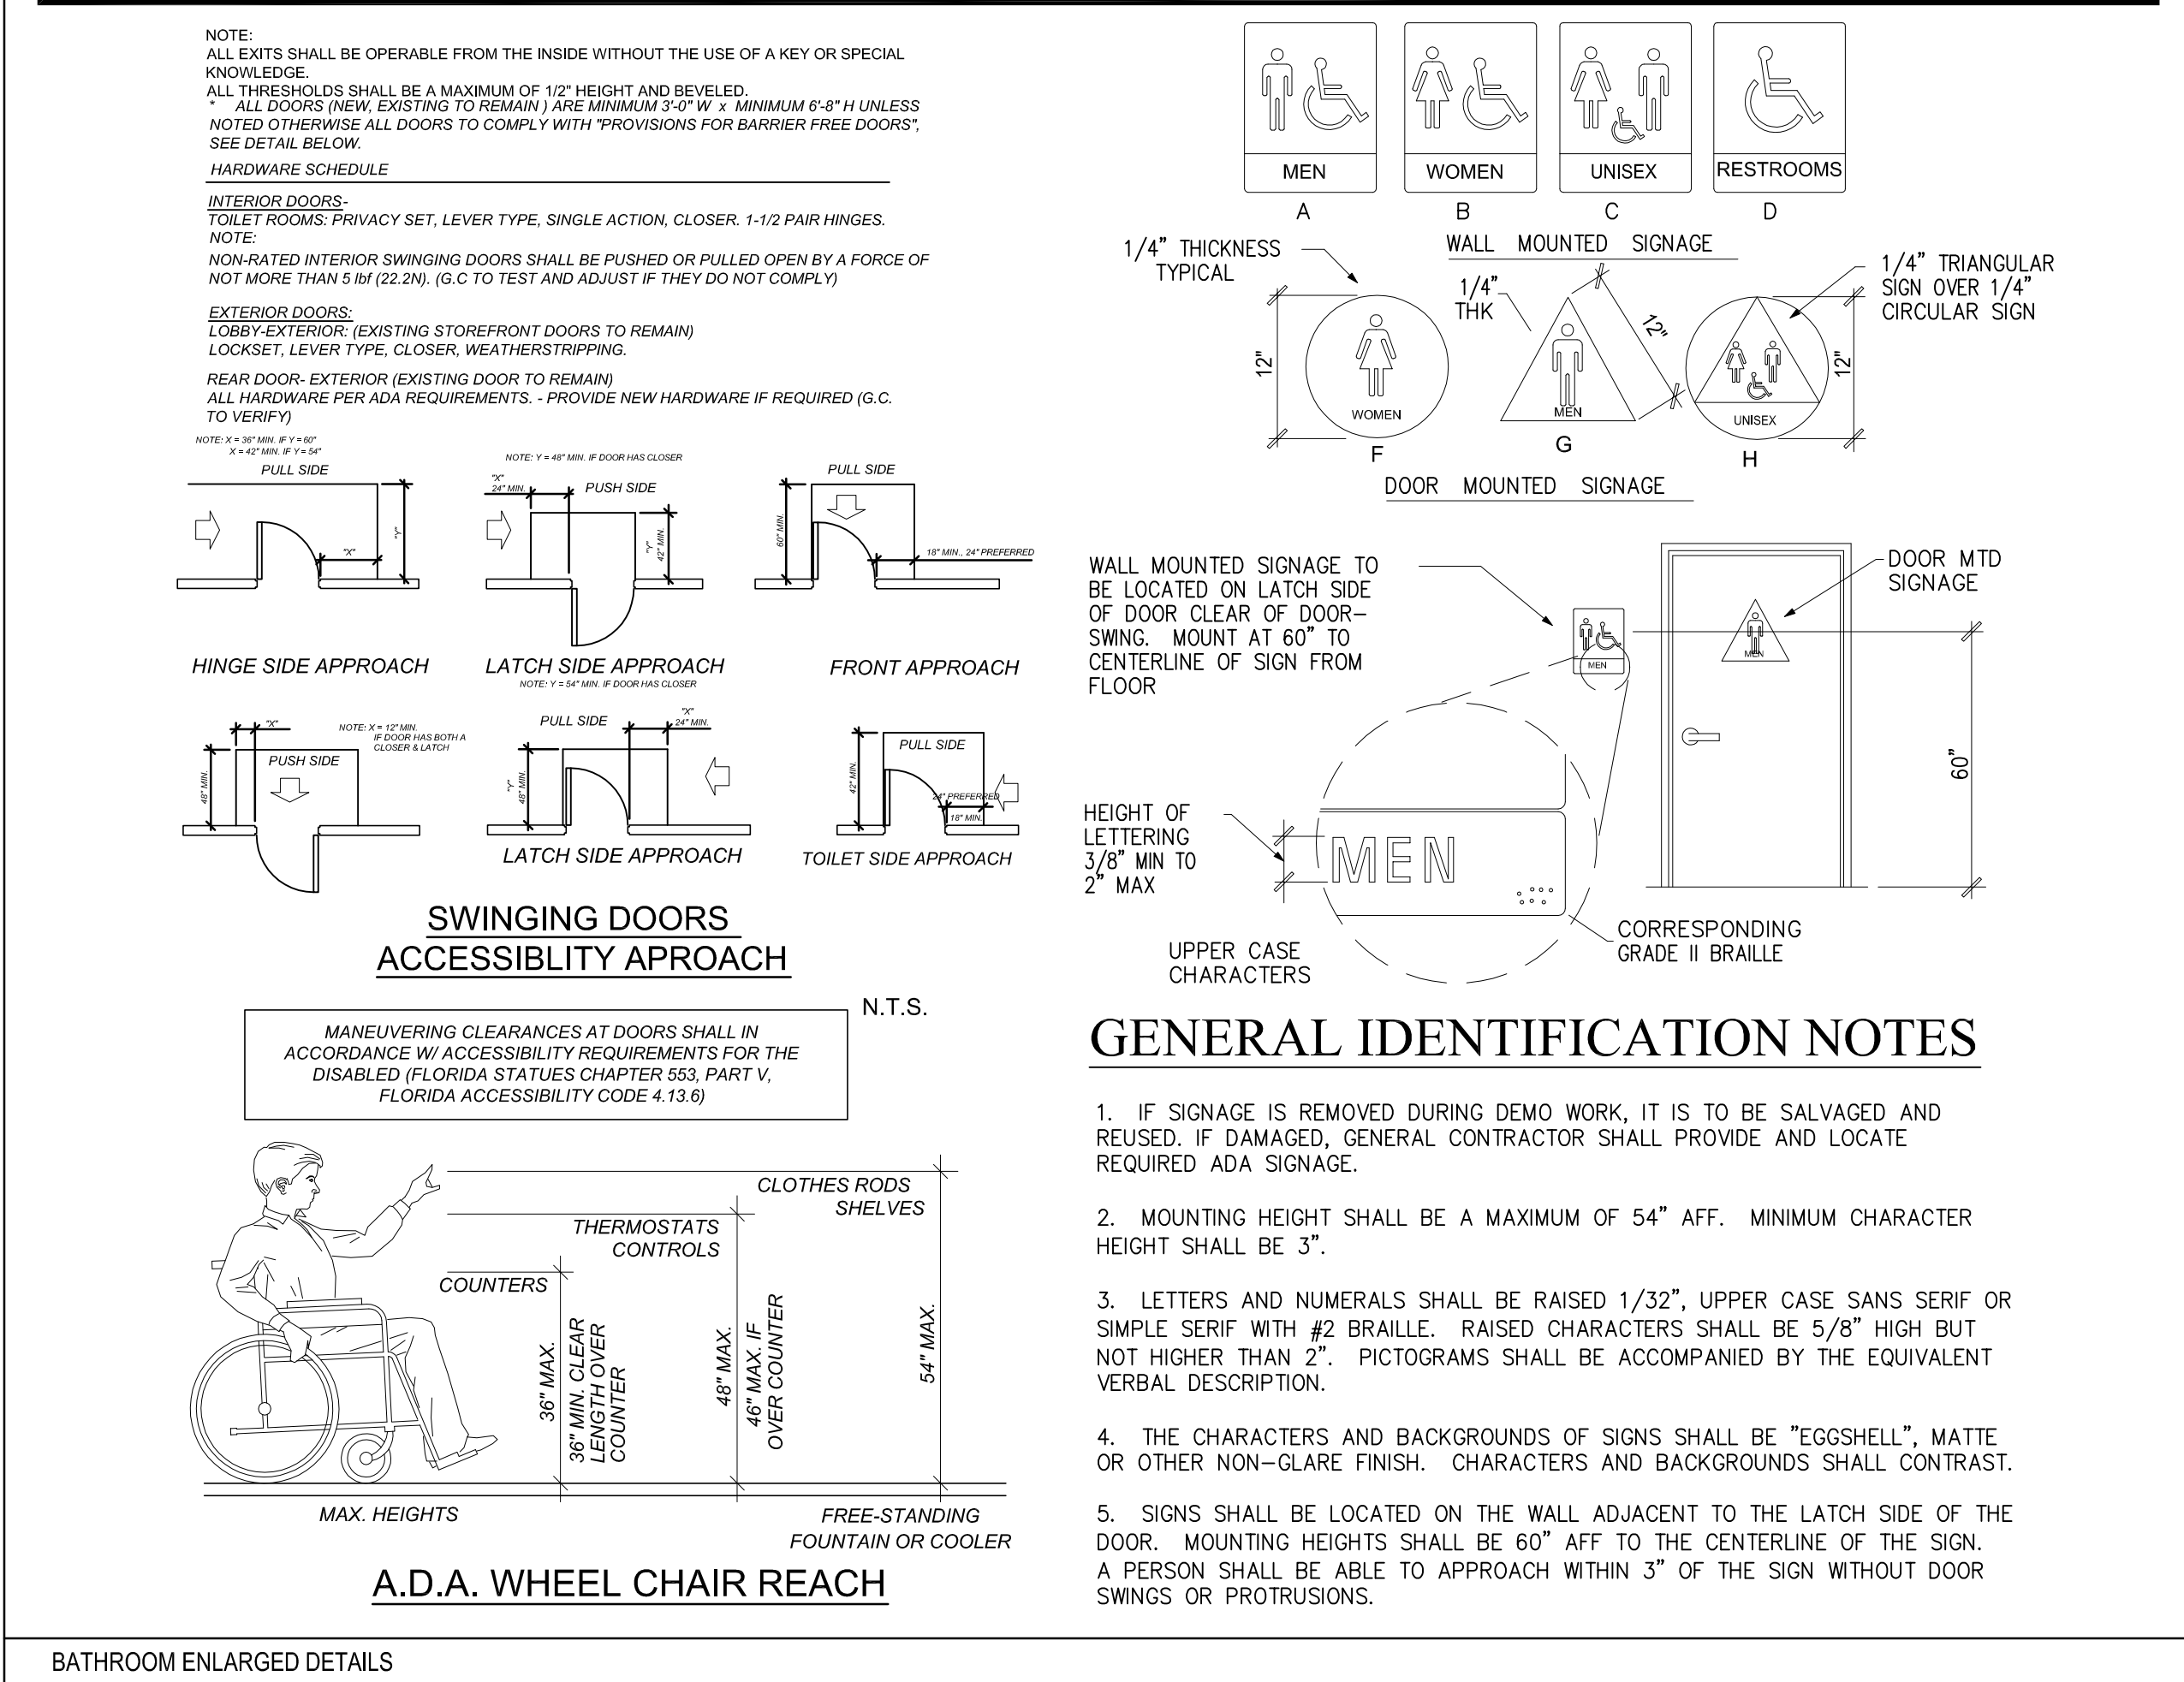

ELECTRICAL KEY

- CLG
 - AF
 - WP
 - DED.
 - GFI
 - 220V
 - DISPOSAL
 - WALL SWITCH
 - THREE-WAY SWITCH
 - DIMMER SWITCH
 - SURFACE MOUNTED LED LIGHT FIXTURE
 - WALL MOUNTED LED. LIGHT FIXTURE
 - RECESSED LED LIGHT FIXTURE
 - RECESSED LED LIGHT FIXTURE - VAPOR PROOF
 - RECESSED WALL WASHER LIGHT FIXTURE
 - PENDANT FIXTURE
 - FLUORESCENT LIGHT FIXTURE
 - EXHAUST FAN
 - EXHAUST FAN/LIGHT COMBINATION
 - EXTERIOR GOOSENECK DOWNLIGHT
 - CHANDELIER
 - SMOKE DETECTOR
 - OCCUPANCY SENSOR SWITCH
 - TELEPHONE
 - DATA/COMMUNICATIONS PORT
 - TELEVISION (OPTIONAL)
 - THERMOSTAT
 - ELECTRIC METER
 - INSTANT WATER HEATER
 - ELECTRIC PANEL
 - DISCONNECT SWITCH
 - SECURITYSYSTEM KEYPAD
 - SPEAKER (OPTIONAL)
 - LED ROPE LIGHT - COVE LIGHT WITH RGB DX CONTROLLER
 - CEILING FAN
 - LED TRACK LIGHT FIXTURE
 - CANOPY MOUNTED BUILDING UPLIGHTING
 - SECURITY/FLOOD LIGHTS (w/MOTION)
 - LANDSCAPE FLOOD LIGHT
 - SURFACE MOUNTED JUNCTION BOX
 - FLUORESCENT LIGHT FIXTURE
- DUPLUX CONVENIENCE OUTLET
DUPLUX CEILING OUTLET
DUPLUX ARC FAULT OUTLET
DUPLUX OUTLET ABOVE COUNTER
WEATHERPROOF DUPLUX OUTLET
DEDICATED OUTLET
GROUND FAULT INTERRUPTER DUPLUX OUTLET
HALF-SWITCHED DUPLUX OUTLET
DUPLUX OUTLET IN FLOOR
220 VOLT OUTLET
- RECESSED LED LIGHT FIXTURE - VAPOR PROOF
- RECESSED WALL WASHER LIGHT FIXTURE
- PENDANT FIXTURE
- FLUORESCENT LIGHT FIXTURE
- EXHAUST FAN
- EXHAUST FAN/LIGHT COMBINATION
- EXTERIOR GOOSENECK DOWNLIGHT
- CHANDELIER
- SMOKE DETECTOR
- OCCUPANCY SENSOR SWITCH
- TELEPHONE
- DATA/COMMUNICATIONS PORT
- TELEVISION (OPTIONAL)
- THERMOSTAT
- ELECTRIC METER
- INSTANT WATER HEATER
- ELECTRIC PANEL
- DISCONNECT SWITCH
- SECURITYSYSTEM KEYPAD
- SPEAKER (OPTIONAL)
- LED ROPE LIGHT - COVE LIGHT WITH RGB DX CONTROLLER
- CEILING FAN
- LED TRACK LIGHT FIXTURE
- CANOPY MOUNTED BUILDING UPLIGHTING
- SECURITY/FLOOD LIGHTS (w/MOTION)
- LANDSCAPE FLOOD LIGHT
- SURFACE MOUNTED JUNCTION BOX
- FLUORESCENT LIGHT FIXTURE

LIGHTING & ELECTRICAL SCHEDULE

SCALE: 1/4"=1'-0"


22

DETAIL

SCALE: 1/4"=1'-0"

21

REFLECTED CEILING PLAN

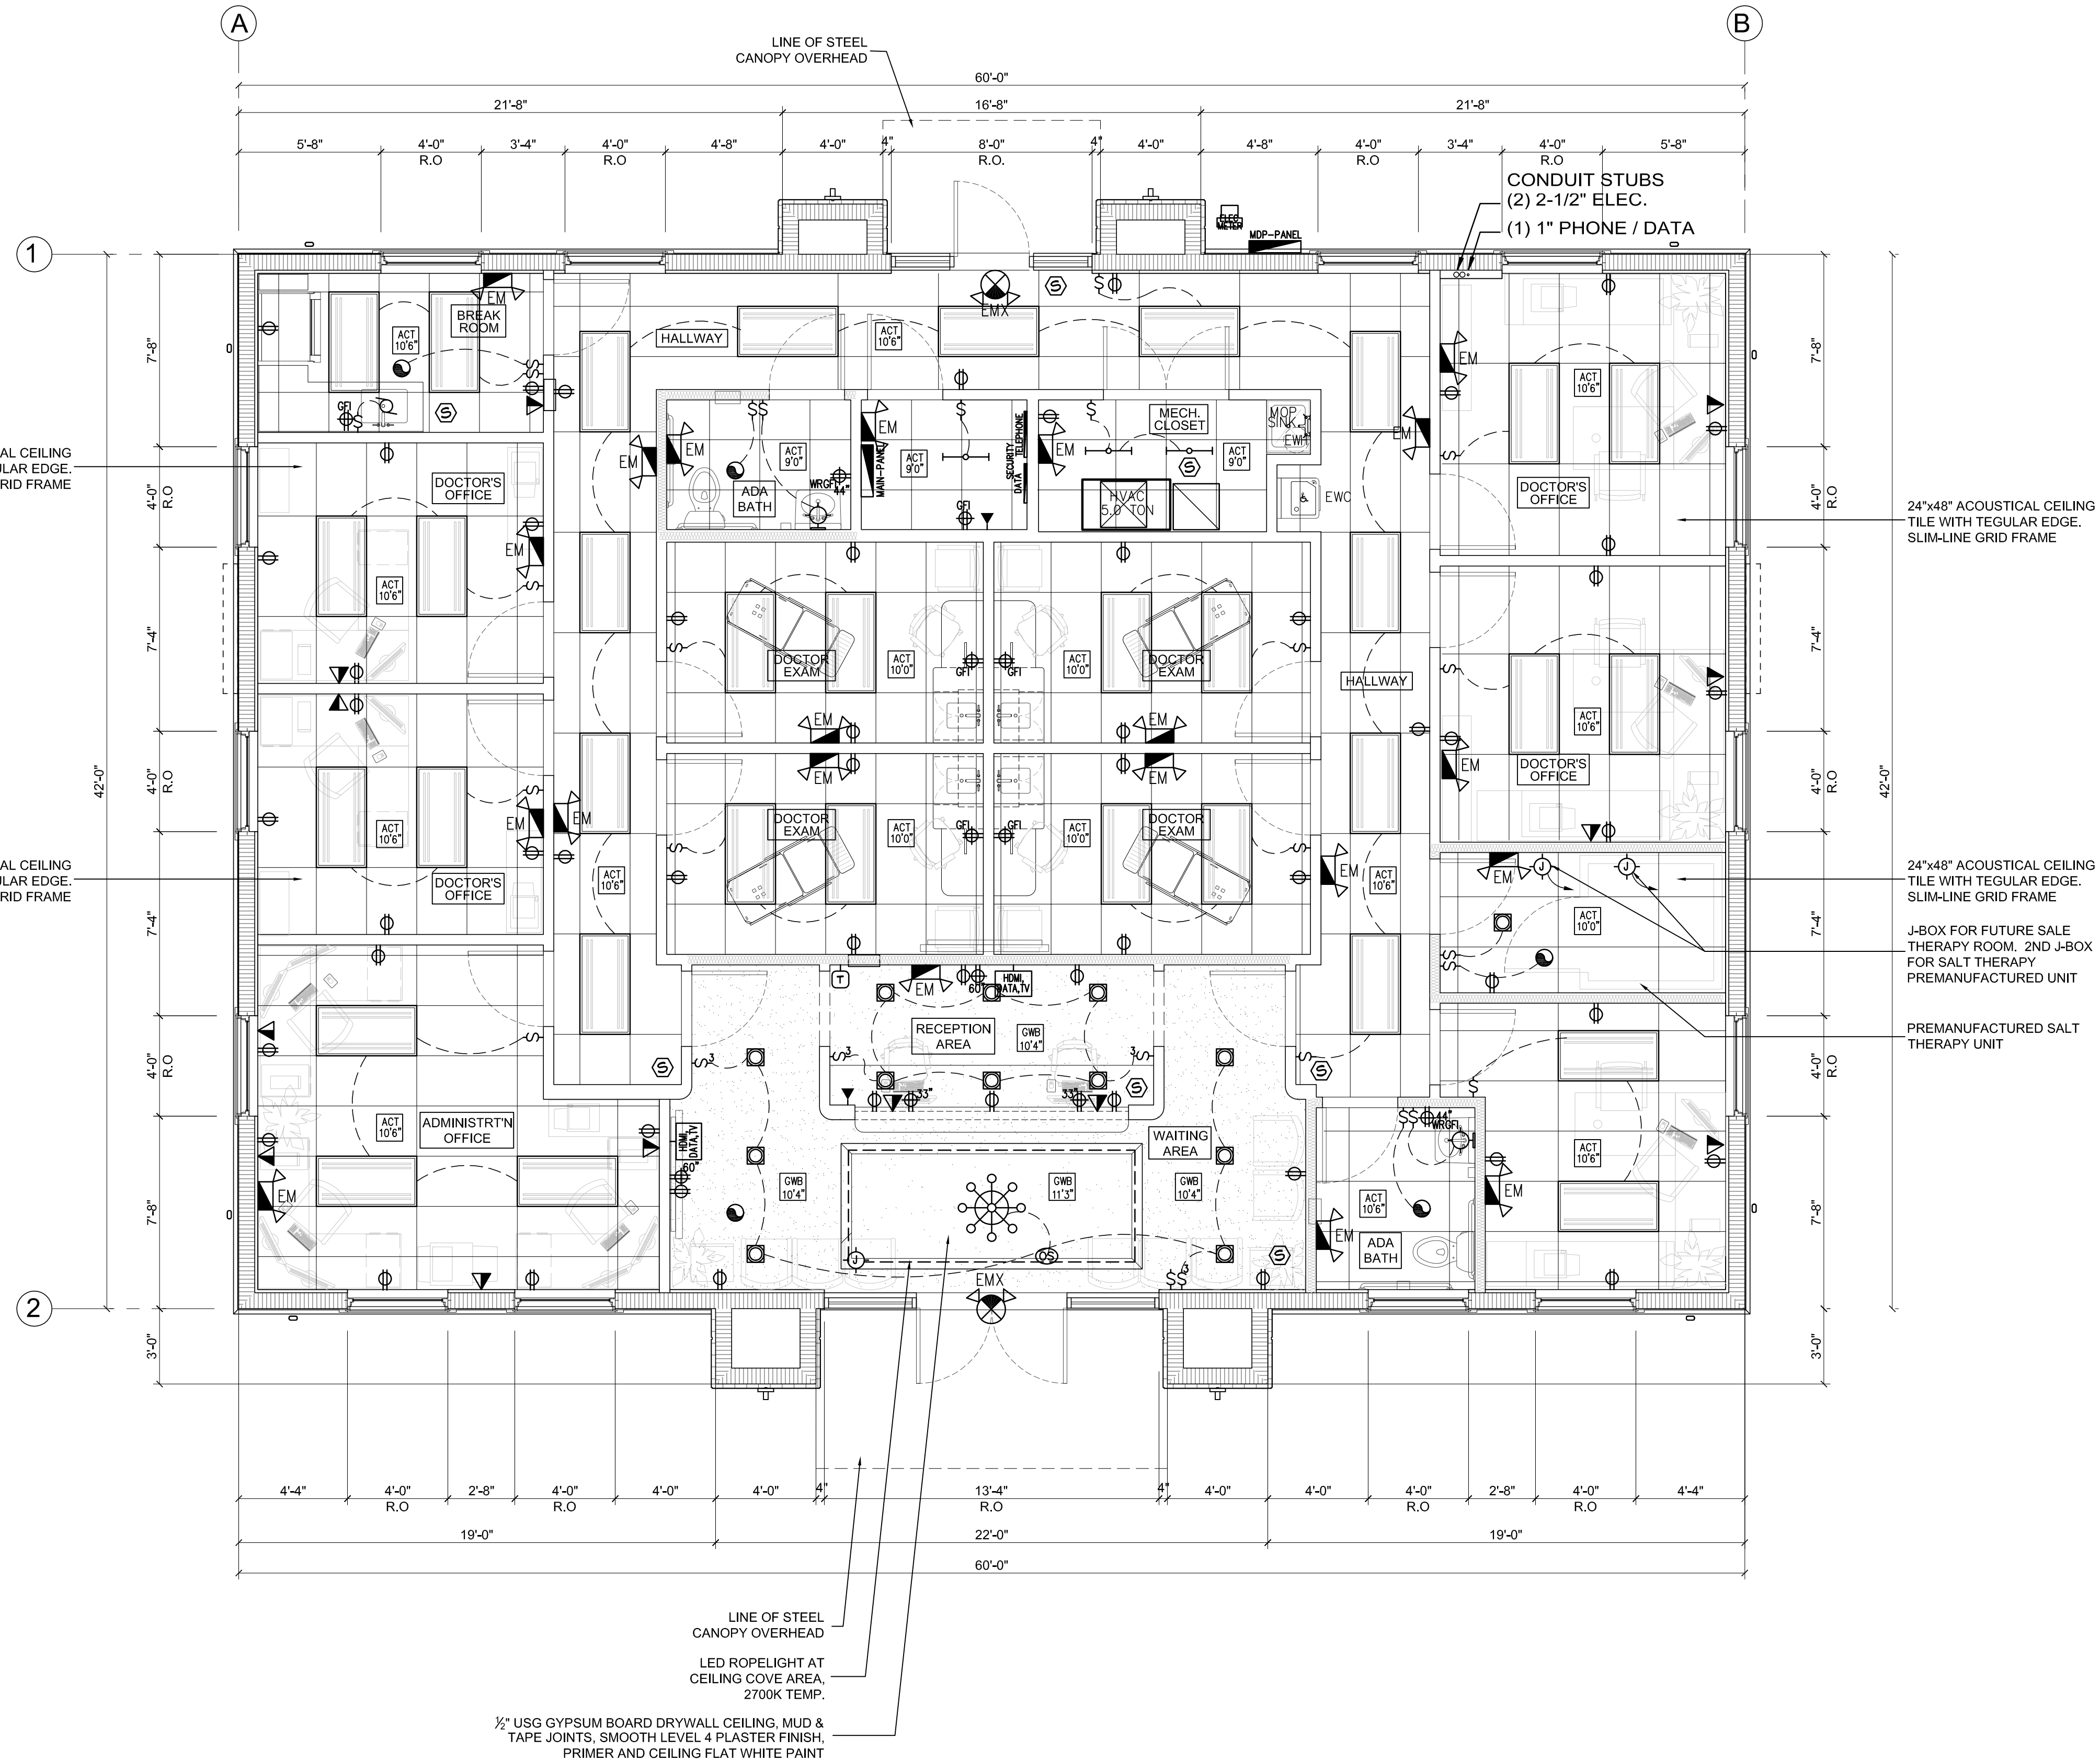


SCALE: 1/4"=1'-0"

01



REVISIONS		
#	DATE	DESCRIPTION
1	02/21/26	SUBMIT

DRAWN BY: AFS
CHECKED BY: AFS
DATE: FEBRUARY 21, 2026

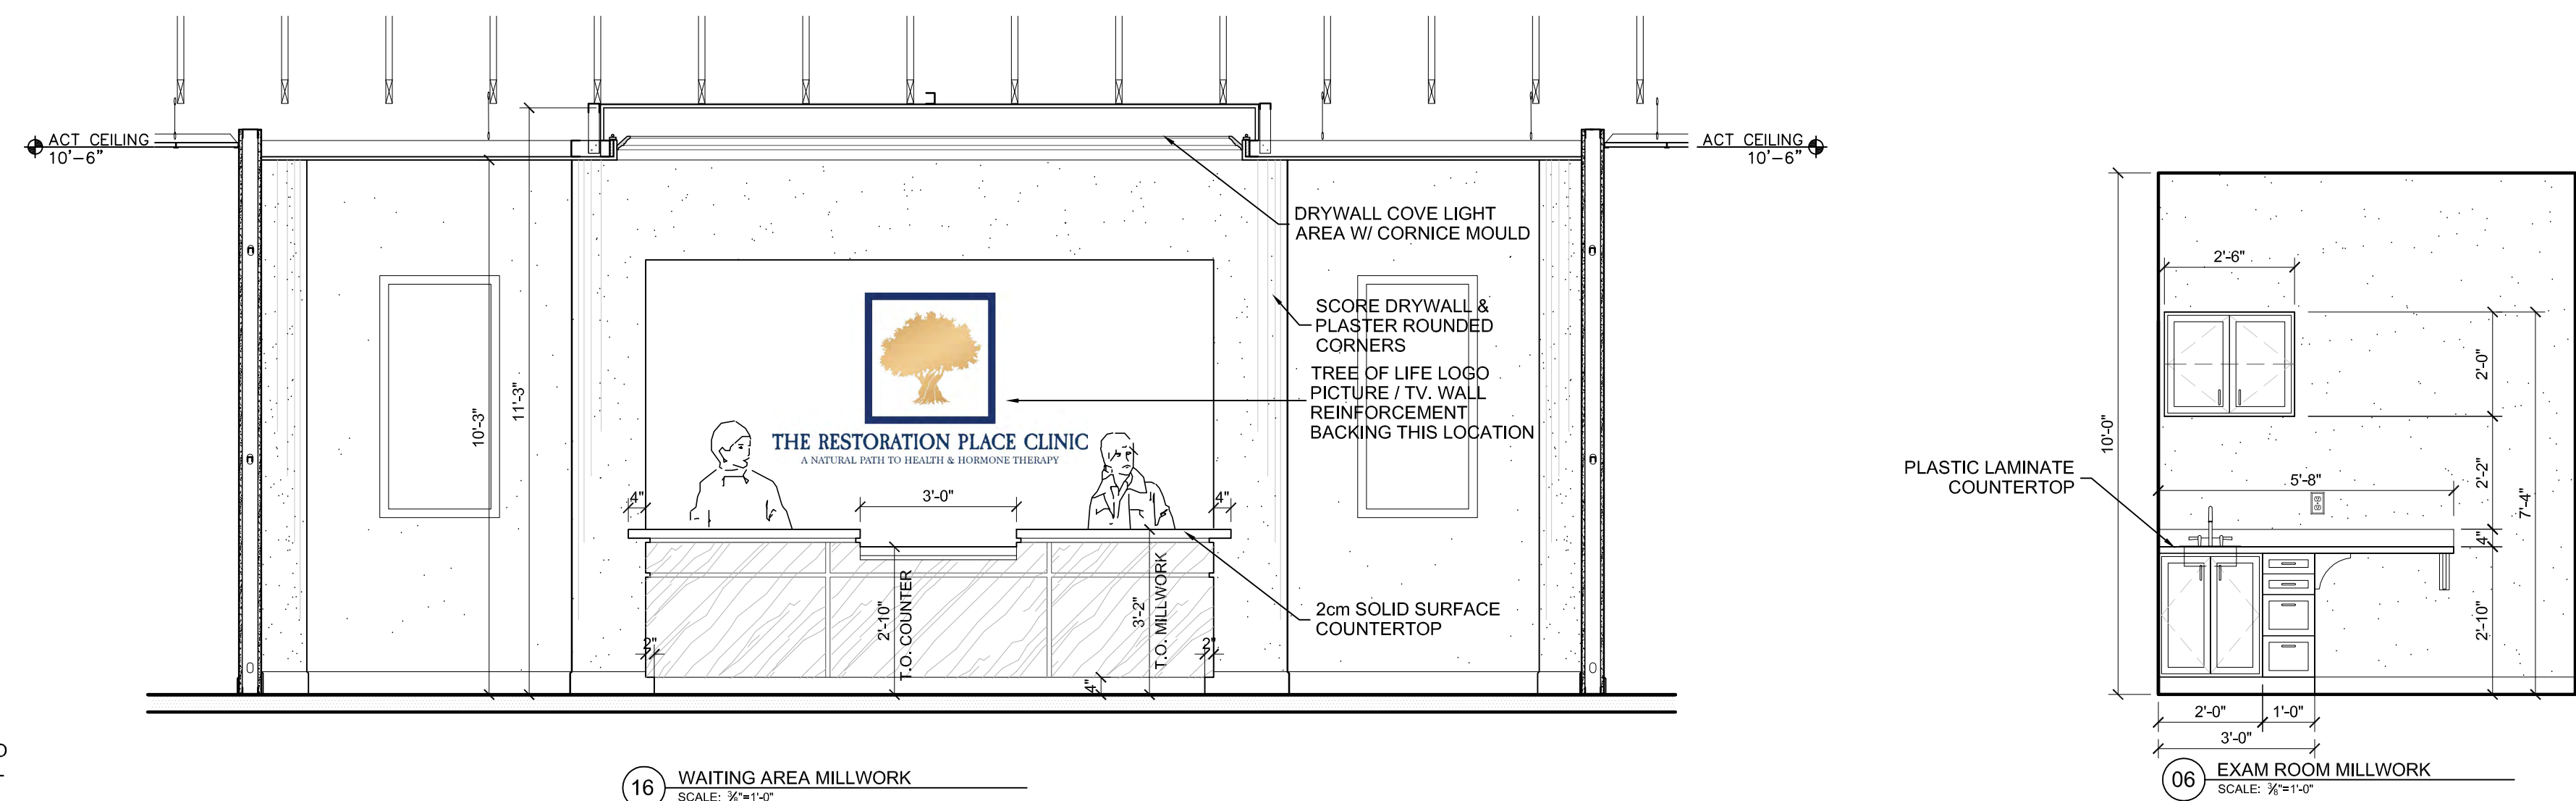

FLOOR FINISH SCHEDULE		STANDARD FLOOR FINISHES			
TAG	DESCRIPTION	MANUF.	MODEL	LOCATION	REMARK
(F-1)	LUXURY VINYL TILE 4" x48" PLANKS	ALOFT LVT GLUEDOWN	LODGE PLANK GREY PEARL 151 P151G	EXAM ROOM PUBLIC SPACES	
(F-2)	LUXURY VINYL TILE 4" x48" PLANKS	FLOOR & DECOR	OWNER SELECT	ADA BATHROOMS <0.60 SLIP COEFFICIENT	MUST MEET ADA SLIP COEFFICIENT < 0.60 COEF. WET; GROUT SEALER
(F-3)	SEALED CONCRETE FLOOR	CONTRACTOR SELECT	CONTRACTOR SELECT	MECHANICAL ROOM ELECTRICAL CLOSET	
(F-4)					
(F-5)					
(F-6)					
(F-7)					
(F-8)					
(F-9)					

Architectural floor plan of a medical suite, showing various rooms and their dimensions. The plan is oriented with a north arrow pointing towards the top-left corner.

Rooms and Features:

- DOCTOR'S OFFICE:** Multiple offices, each with a desk, chair, and filing cabinets. Dimensions range from 7'-4" to 7'-8".
- DOCTOR EXAM:** Examination rooms with a desk, chair, and medical equipment. Dimensions range from 7'-4" to 7'-8".
- ADMIN. OFFICE:** Administrative office with a desk and chair. Dimensions: 7'-8" x 4'-0".
- WAITING AREA:** Central area for patients, featuring a reception desk and seating. Dimensions: 13'-4" x 22'-0".
- RECEPTION / INTAKE:** Area for patient intake, featuring a desk and chair. Dimensions: 4'-0" x 4'-0".
- PLASTIC LAMINATE COUNTERTOP:** Countertop area for medical procedures. Dimensions: 4'-0" x 4'-0".
- SCORE DRYWALL & PLASTER ROUNDED CORNERS:** Area for wall treatment. Dimensions: 4'-0" x 4'-0".
- 2cm SOLID SURFACE COUNTERTOP:** Countertop area for medical procedures. Dimensions: 4'-0" x 4'-0".
- ADA RESTROOM:** Restroom for disabled patients. Dimensions: 4'-0" x 4'-0".
- MECH. CLOSET:** Mechanical closet. Dimensions: 4'-0" x 4'-0".
- HVAC SPLIT:** Heating and air conditioning unit. Dimensions: 4'-0" x 4'-0".
- DATA TELEPHONE:** Telephone for data communication. Dimensions: 4'-0" x 4'-0".
- MAIN-PANEL:** Main electrical panel. Dimensions: 4'-0" x 4'-0".
- SECURITY CLOSET:** Closet for security equipment. Dimensions: 4'-0" x 4'-0".
- DOCTOR'S OFFICE:** Office for the doctor, featuring a desk, chair, and filing cabinets. Dimensions: 7'-4" x 7'-8".
- DOCTOR EXAM:** Examination room for the doctor, featuring a desk, chair, and medical equipment. Dimensions: 7'-4" x 7'-8".
- ADMIN. OFFICE:** Administrative office, featuring a desk, chair, and filing cabinets. Dimensions: 7'-8" x 4'-0".
- WAITING AREA:** Area for patients to wait, featuring a desk and chair. Dimensions: 13'-4" x 22'-0".
- RECEPTION / INTAKE:** Area for patient intake, featuring a desk and chair. Dimensions: 4'-0" x 4'-0".
- PLASTIC LAMINATE COUNTERTOP:** Countertop area for medical procedures. Dimensions: 4'-0" x 4'-0".
- SCORE DRYWALL & PLASTER ROUNDED CORNERS:** Area for wall treatment. Dimensions: 4'-0" x 4'-0".
- 2cm SOLID SURFACE COUNTERTOP:** Countertop area for medical procedures. Dimensions: 4'-0" x 4'-0".
- ADA RESTROOM:** Restroom for disabled patients. Dimensions: 4'-0" x 4'-0".
- MECH. CLOSET:** Mechanical closet. Dimensions: 4'-0" x 4'-0".
- HVAC SPLIT:** Heating and air conditioning unit. Dimensions: 4'-0" x 4'-0".
- DATA TELEPHONE:** Telephone for data communication. Dimensions: 4'-0" x 4'-0".
- MAIN-PANEL:** Main electrical panel. Dimensions: 4'-0" x 4'-0".
- SECURITY CLOSET:** Closet for security equipment. Dimensions: 4'-0" x 4'-0".


Dimensions:

- Overall Dimensions:** 60'-0" (width) x 42'-0" (depth).
- Room Dimensions:**
 - DOCTOR'S OFFICE: 7'-4" x 7'-8"
 - DOCTOR EXAM: 7'-4" x 7'-8"
 - ADMIN. OFFICE: 7'-8" x 4'-0"
 - WAITING AREA: 13'-4" x 22'-0"
 - RECEPTION / INTAKE: 4'-0" x 4'-0"
 - PLASTIC LAMINATE COUNTERTOP: 4'-0" x 4'-0"
 - SCORE DRYWALL & PLASTER ROUNDED CORNERS: 4'-0" x 4'-0"
 - 2cm SOLID SURFACE COUNTERTOP: 4'-0" x 4'-0"
 - ADA RESTROOM: 4'-0" x 4'-0"
 - MECH. CLOSET: 4'-0" x 4'-0"
 - HVAC SPLIT: 4'-0" x 4'-0"
 - DATA TELEPHONE: 4'-0" x 4'-0"
 - MAIN-PANEL: 4'-0" x 4'-0"
 - SECURITY CLOSET: 4'-0" x 4'-0"

Notes:

- CONDUIT STUBS (2) 2-1/2" ELEC.
- (1) 1" PHONE / DATA


PARTITION TYPES

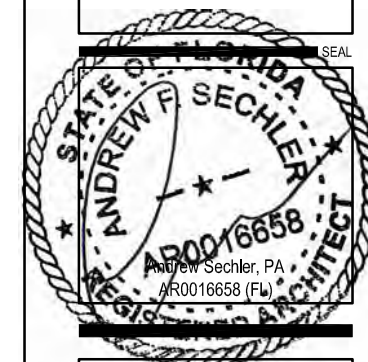

REVISIONS		
#	DATE	DESCRIPTION
1	02/21/25	SUBMIT

DRAWN BY: AFS
CHECKED BY: AFS
DATE: FEBRUARY 21, 2025

SHEET:
A
500
Elite Universal Job No.
90210

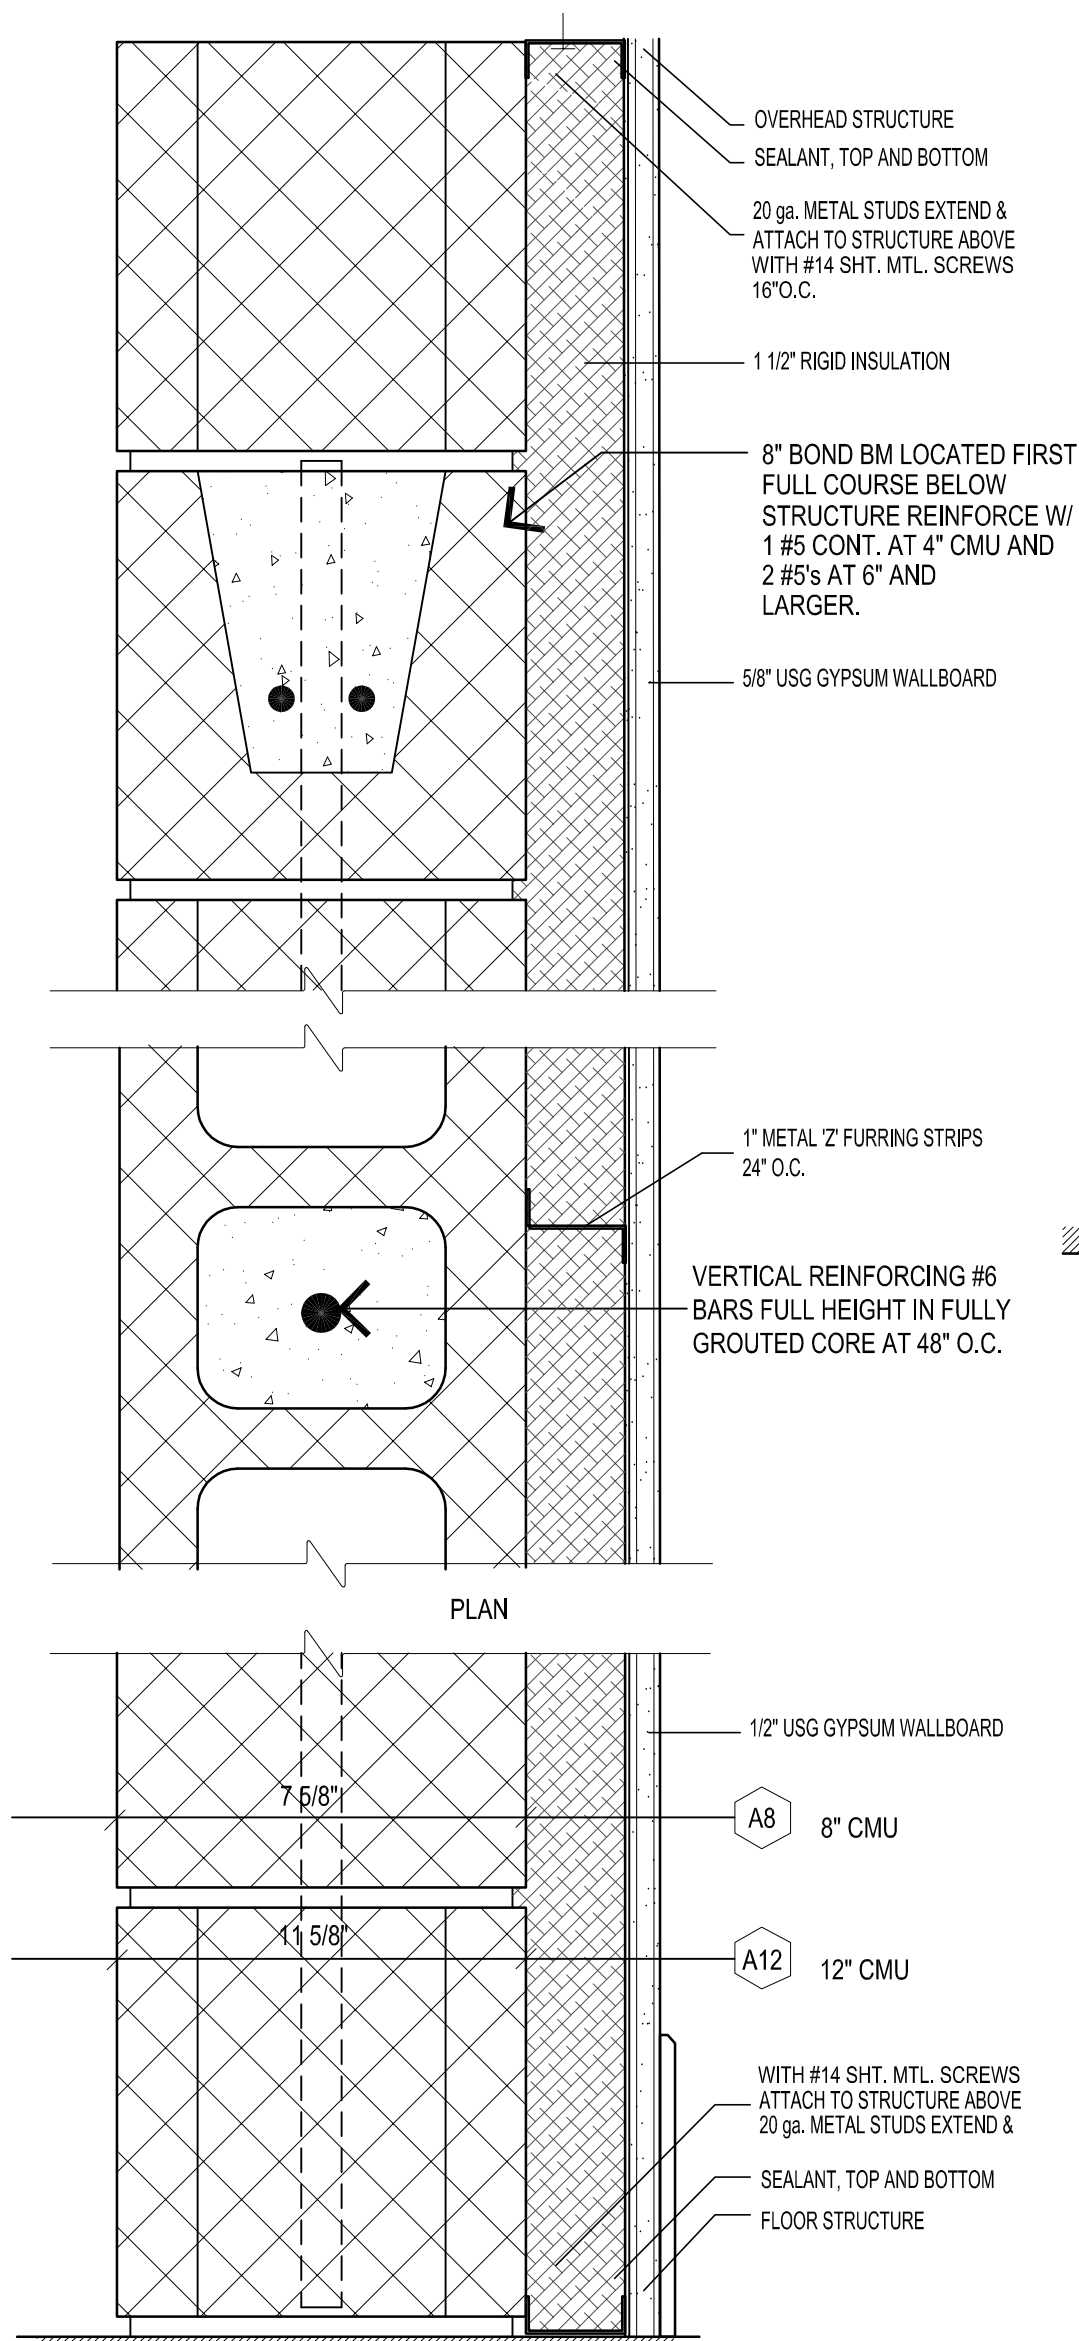


PARTITION TYPE A: 1" 20ga METAL STUDS AT 24" O.C.
WITH ONE LAYER OF 1/2" GYP BD ONE SIDE.
PARTITION TYPE A : CONCRETE MASONRY UNIT BLOCK WITH
HORIZONTAL JOINT REINFORCING AT 16" O.C. VERTICAL.

PARTITION TYPE	* LIMITING HEIGHT	* FIRE RATING	STC RATING
A8	11'-8"	AND 4 HR RATING BASED ON UL DESIGNS U901, U902, U904, U905, U906, & U907.	49
A12	19'-0"		--


* LIMITING HEIGHTS AND FIRE RATING MAY VARY
DEPENDENT ON GOVERNING CODE.

FIRE RATED WALL U905
PARTITION TYPE A

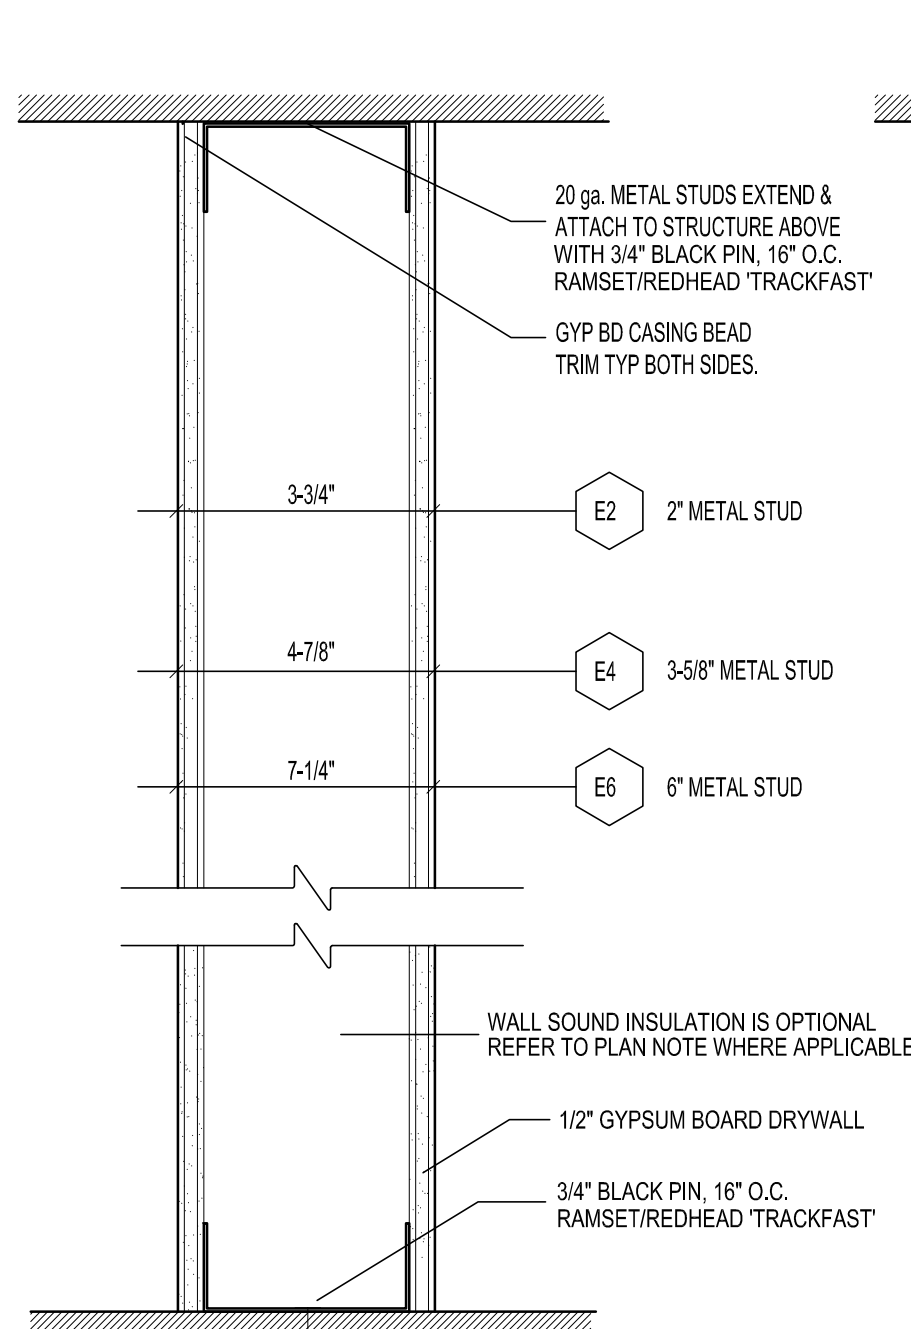


PARTITION TYPE	* LIMITING HEIGHT	* FIRE RATING	STC RATING
E2	10'-9"	-	35
E4	14'-3"	-	40
E6	15'-0"	-	40

PARTITION TYPE E

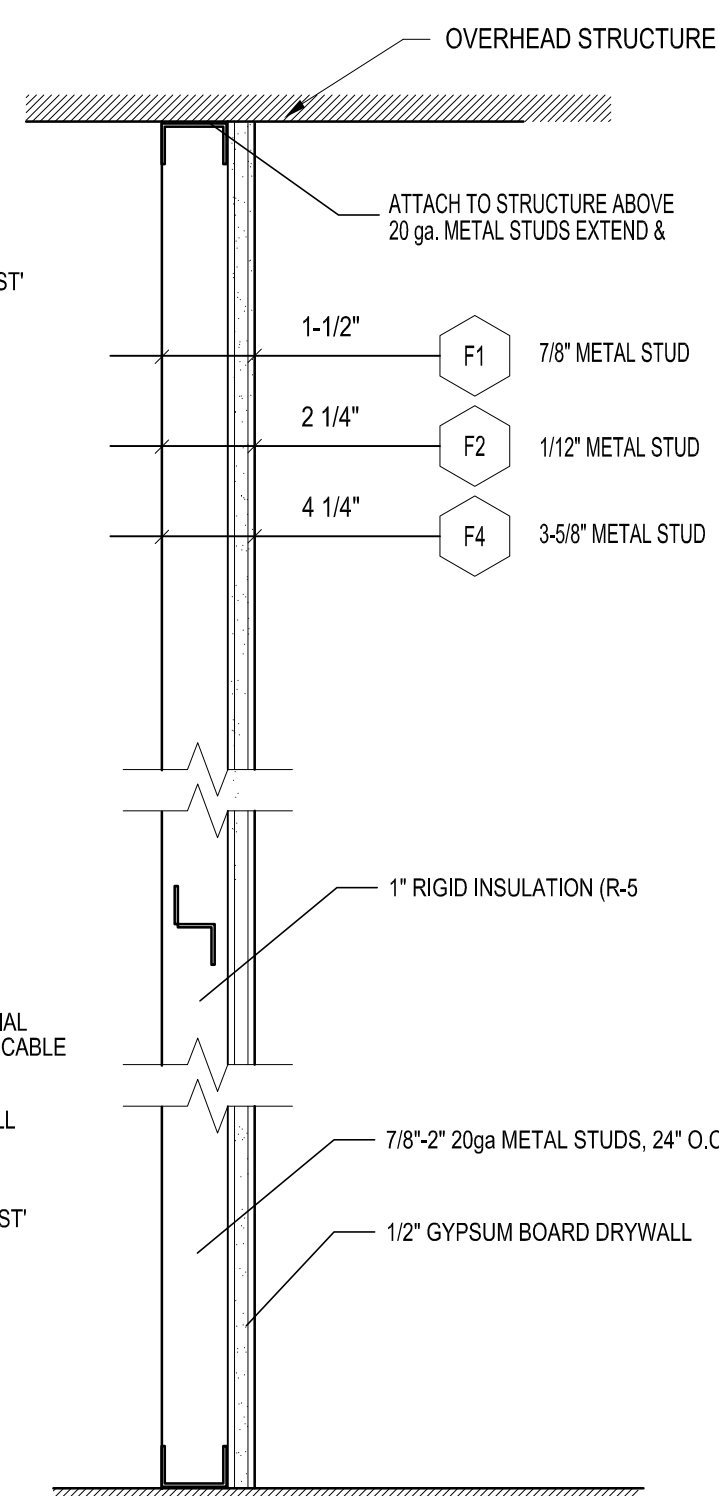


PARTITION TYPE F : METAL STUDS AT 24" O.C.
WITH ONE LAYER OF 1/2" GYP BD ONE SIDE.
1" RIGID INSULATION

PARTITION TYPE F

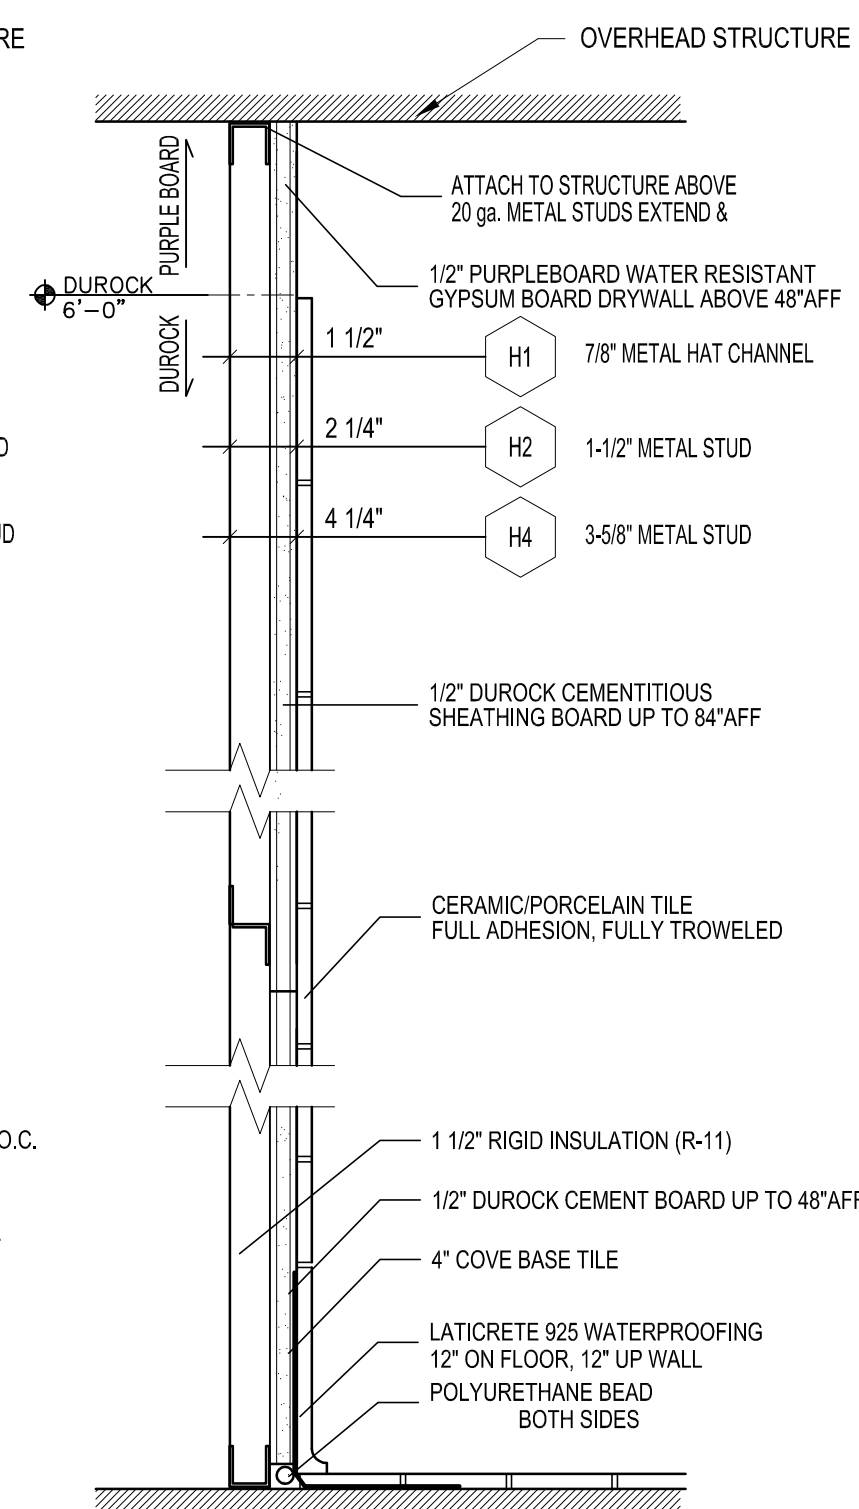


PARTITION TYPE H : METAL STUDS AT 24" O.C.
WITH ONE LAYER OF 1/2" GYP BD/DUROCK & TILE ONE SIDE

PARTITION TYPE H

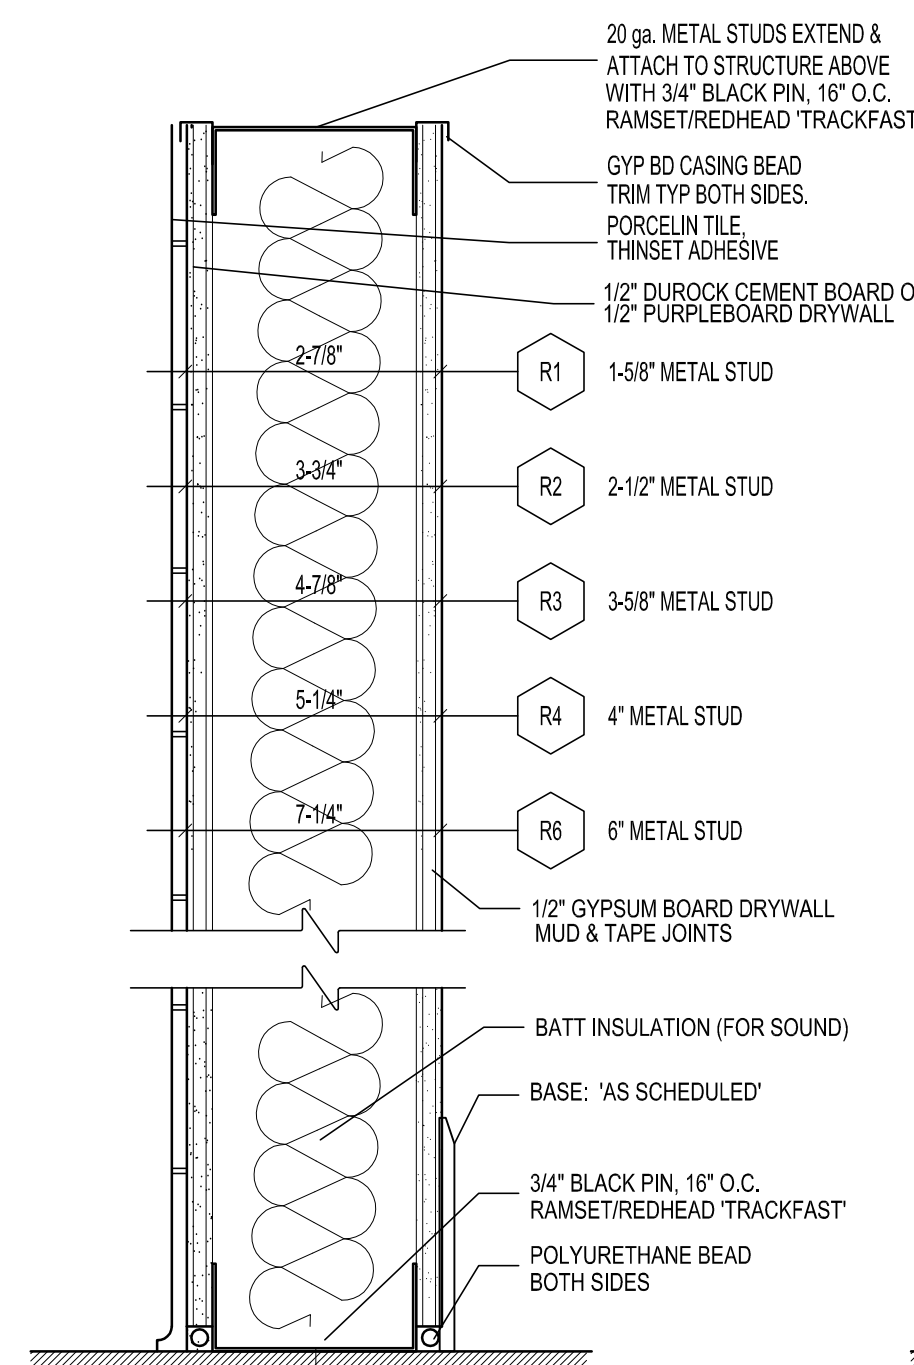


PARTITION TYPE	* LIMITING HEIGHT	* FIRE RATING	STC RATING
R2	10'-9"	-	35
R3	13'-6"	-	40
R4	14'-3"	-	40
R6	15'-0"	-	40

PARTITION TYPE R

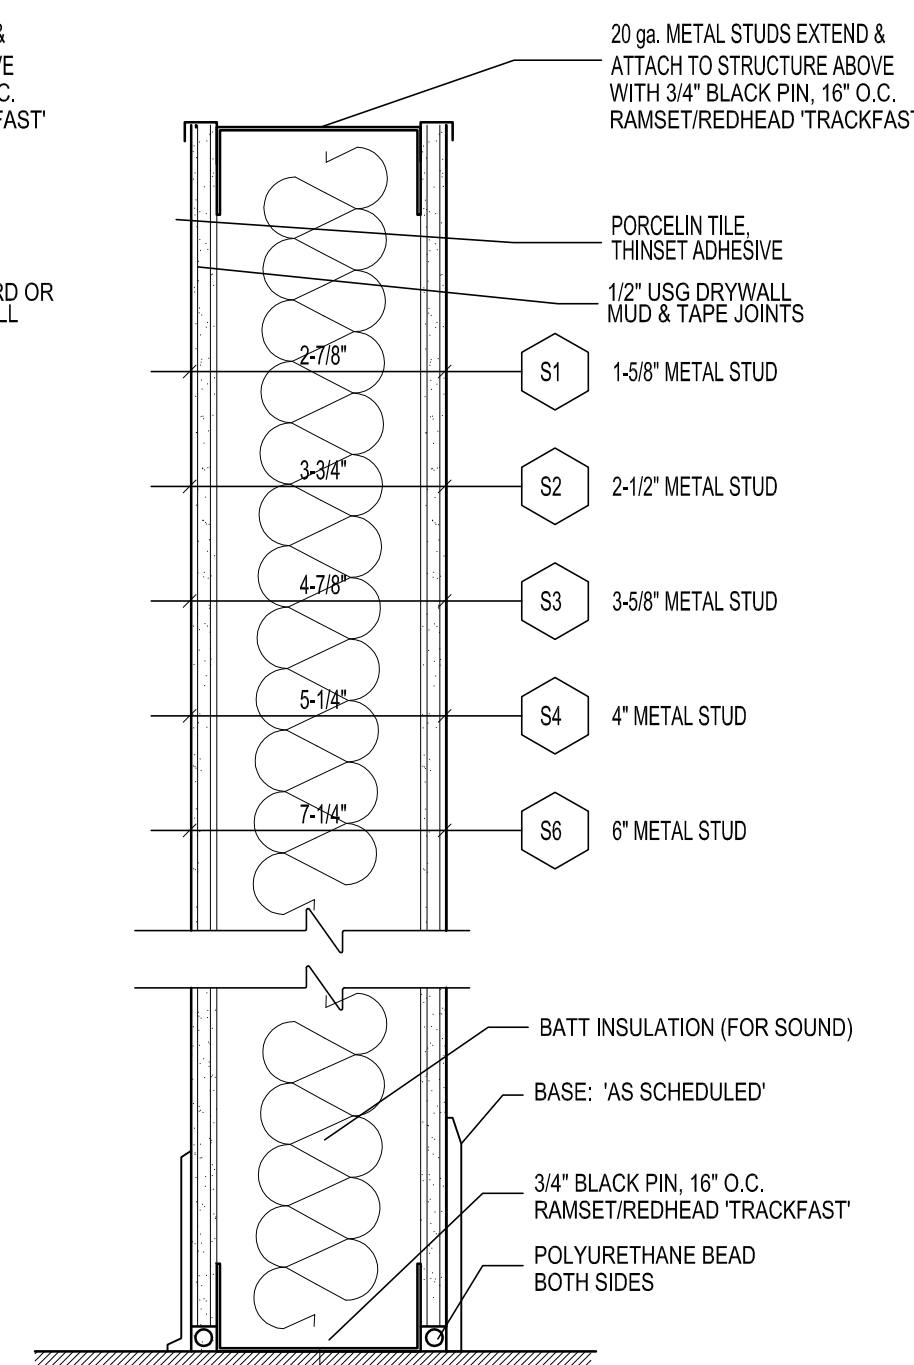

PARTITION TYPE	* LIMITING HEIGHT	* FIRE RATING	STC RATING
S2	10'-9"	-	35
S3	13'-6"	-	40
S4	14'-3"	-	40
S6	15'-0"	-	40

PARTITION TYPE S

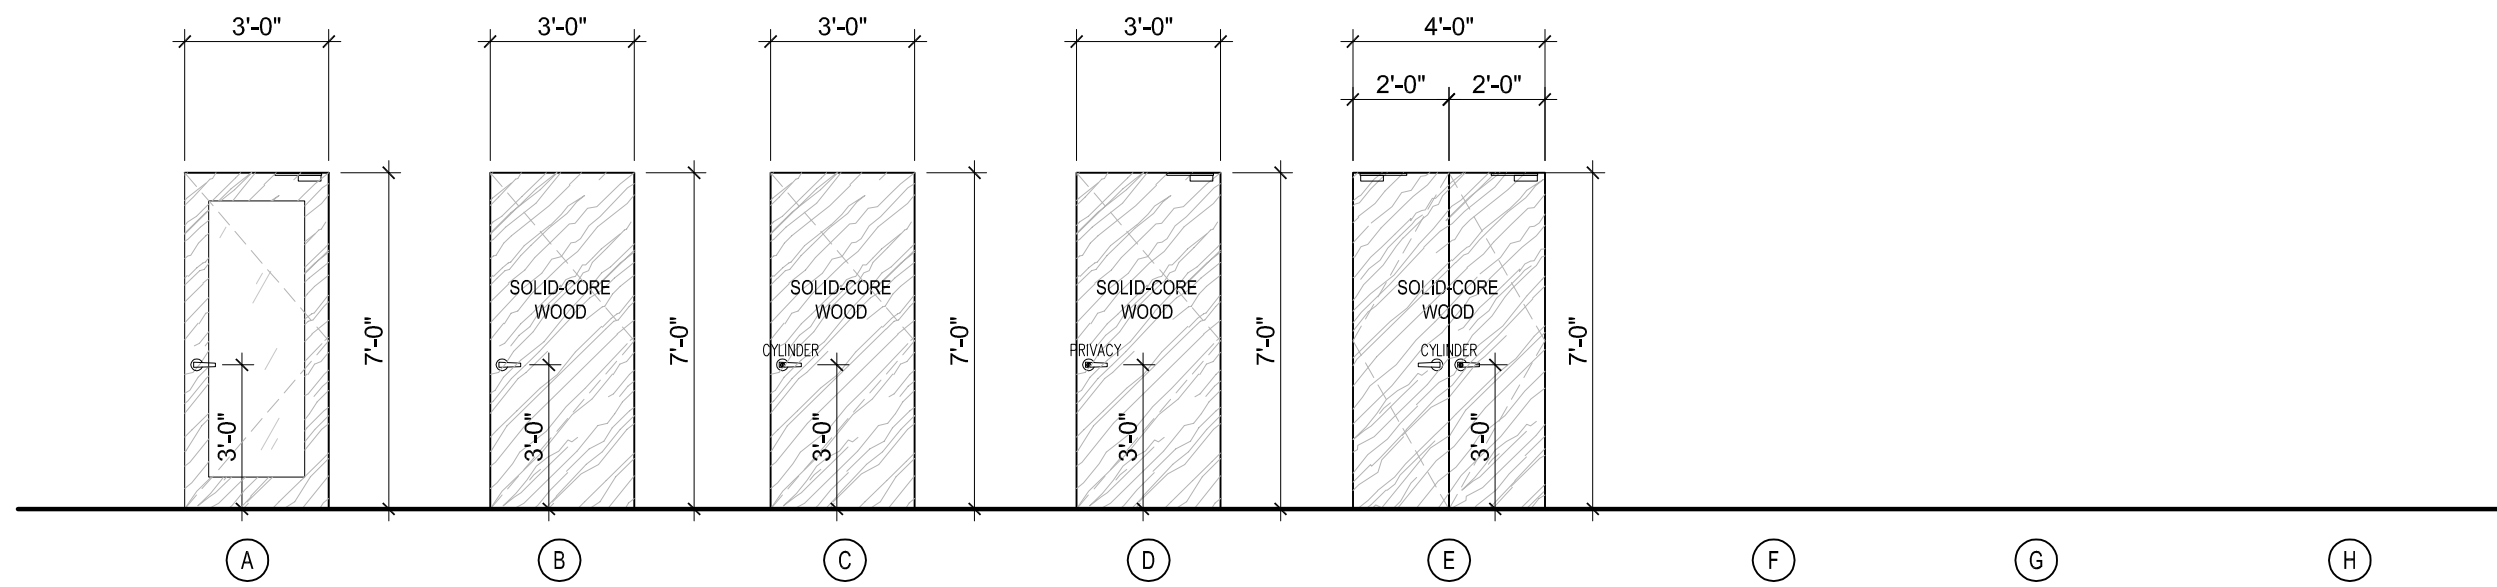[illegible]

METAL DOORS: CECO / DAYBAR
DECORATOR SERIES FLAT-PANEL

STOREFRONT DOORS: CORAL INDUSTRIES, INC.
FL 300 ALUMINUM DOORS.
CLEAR ANODIZED 1" INSULATED GLASS

INTERIOR DOORS: MANUFACTURER
SOLID BIRCH WOOD DOOR. FLAT-PANEL

1. ALL LOCK AND PASSAGE SETS TO BE SCHLAGE SERIES AL GRADE OR BETTER. LOCKS NEED TO BE REKEYABLE.
2. ALL DOORS AND HARDWARE TO COMPLY WITH N.F.P.A. 101
3. PAINT ALL WOOD DOORS AND FRAMES.
4. H.C. DESIGNATES HOLLOW CORE.
5. 3 PANEL DOORS ARE SOLID CORE WOOD DOORS

(1 1/2) PAIR HAGER 4 1/2" x 4 1/2" BUTT
FULL MORTISE HINGES NO. BB1191
FINISH 26D (BLACK)
(1) LEVER HANDLES SCHLAGE "SOLSTICE", J-10 SOL
(1) CLOSER; HAGER 5200 SERIES


(1 1/2) PAIR HAGER 4 1/2 " x4 1/2 "
BUTT FULL MORTISE HINGES NO. BB1191 EA.
FINISH 26D (BLACK)
(1) LEVER HANDLES SCHLAGE "SOLSTICET", J-10 SOL

(1 1/2) PAIR HAGER 4 1/2" x4 1/2"
BUTT FULL MORTISE HINGES NO. BB1191 EA.
FINISH 26D (BLACK)
(1) LEVER HANDLES SCHLAGE "SOLSTICET", J-10 SOL
** **DEVICE HAS CYLINDER LOCK, WITH LEVER HANDLE**
(1) CLOSER - MOUNTED IN ROOM


(1 1/2) PAIR HAGER 4 1/2" x4 1/2" BUTT
FULL MORTISE HINGES NO. BB1191
FINISH 26D (BLACK)
(1) LEVER HANDLES SCHLAGE "SOLSTICET", J-10 SOL
(1) PRIVACY LOCK
(1) CLOSER; HAGER 5200 SERIES

(3) PAIR HAGER 4 1/2" x 4 1/2"
BUTT FULL MORTISE HINGES NO. BB1191 EA.
FINISH 26D (BLACK)
(2) LEVER HANDLES SCHLAGE "SOLSTICET", J-10 SOL
** DEVICE HAS CYLINDER LOCK, WITH LEVER HANDLE
(2) CLOSERS - MOUNTED IN ROOM


SCALE: 1/4"=1'-0"	03
-------------------	----

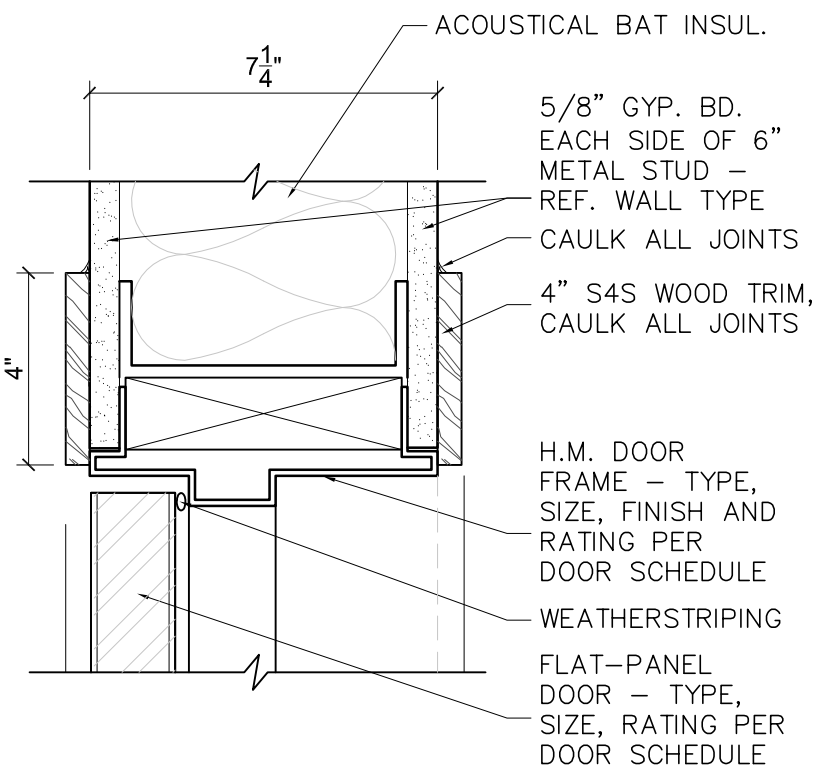


H1/J1 Head/Jamb Detail-Steel
Scale 3"=1'-0"

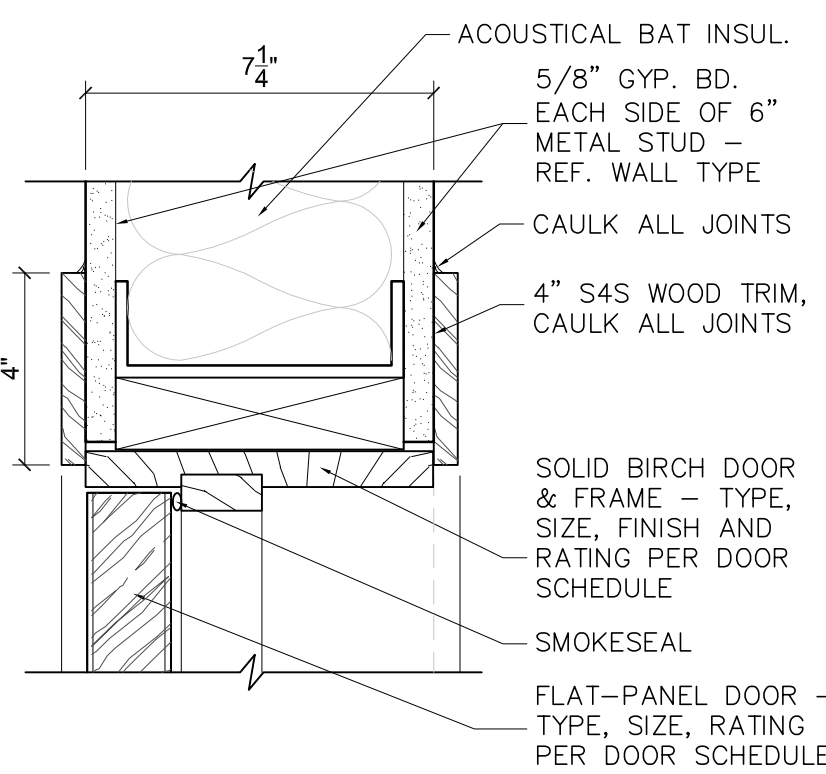


H2/J2 Head/Jamb Detail-Unit Entry
Scale 3/4"=1'-0"

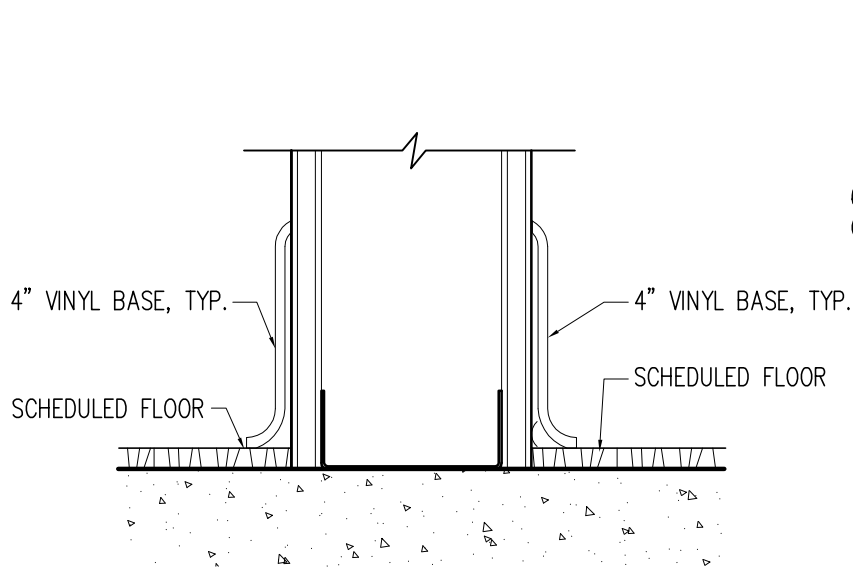


B1 Base Detail
Scale 3"=1'-0"

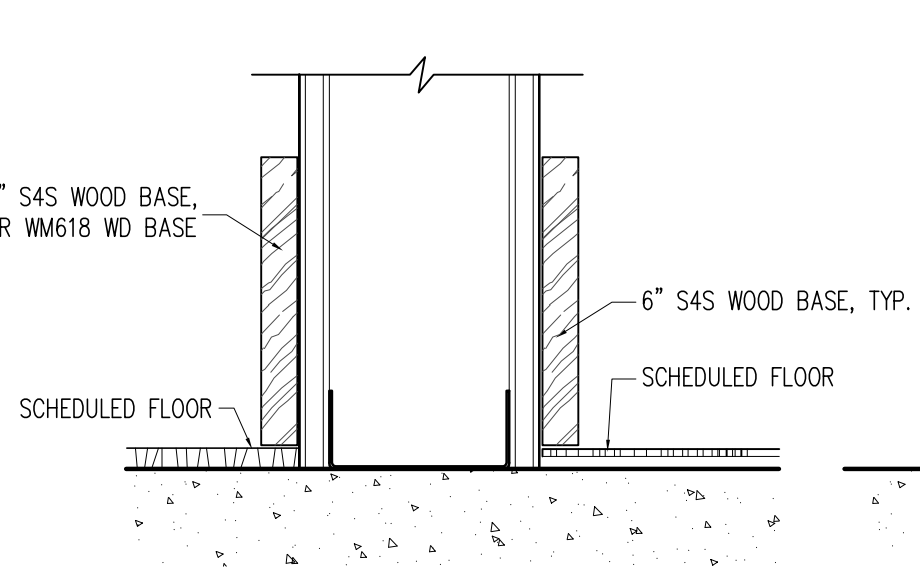


B2 Base Detail
Scale 3"=1'-0"

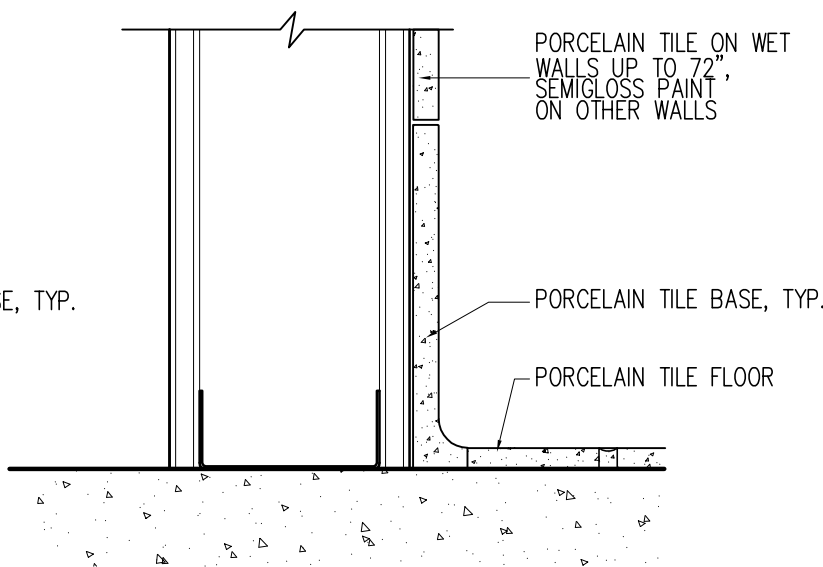


B3 Base Detail
Scale 3"=1'-0"

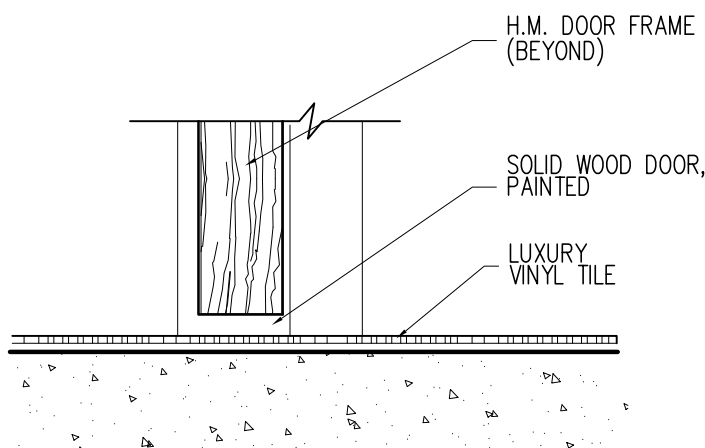

S1 Sill Detail
Scale 3"=1'-0"

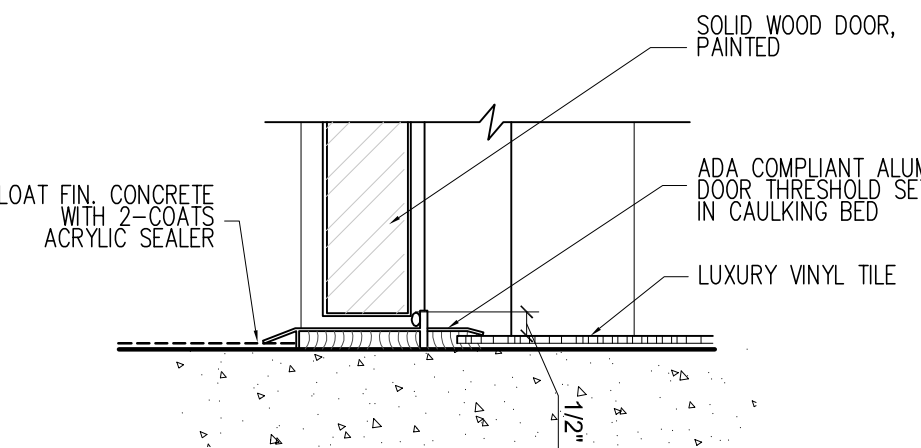

S2 Sill Detail
Scale 3"=1'-0"

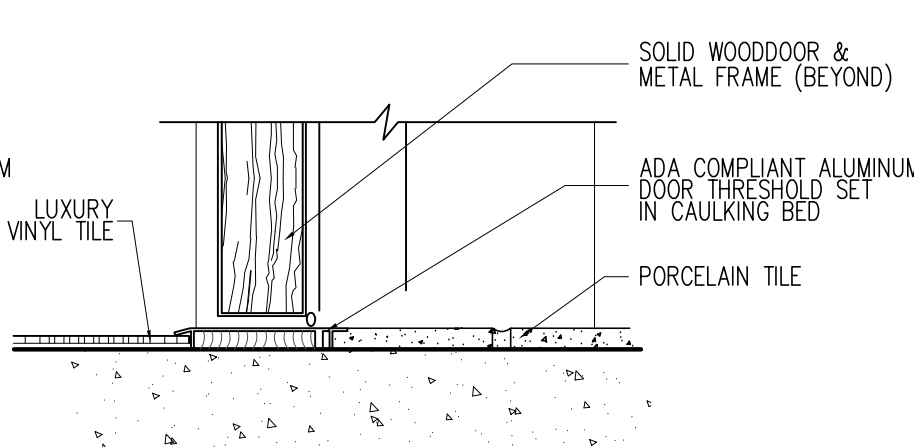


S3 Sill Detail
Scale 3"=1'-0"

SCALE: 3"=1'-0" | 01



MEDICAL OFFICE
SOUTHERN RAILWAY, BLDG #9 OAKLAND, FL 34787

DOOR SCHEDULE AND DETAILS

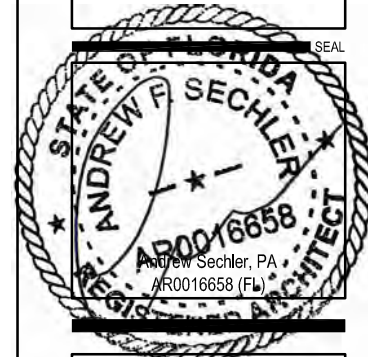

REVISIONS:		
#	DATE	DESCRIPTION
1	02/21/26	SUBMIT
DRAWN BY: AFS		
CHECKED BY: AFS		
DATE: FEBRUARY 21, 2026		

SHEET:
A
520
Elbe Universal Job No.
90210